

DRAWING INDEX SHEET

PAGE LEGEND

AV-X0.0

1 2 3

1 = AUDIO/VISUAL
2 = A: ARCHITECTURAL
F: FLOWS
D: DETAILS
E: ELEVATION
3 = SERIES NUMBER


STANDARD ABBREVIATIONS

A/V	AV INTERFACE	EQ	EQUAL	POTS	PLAIN OLD TELEPHONE SERVICE
AFC	ABOVE FINISH CEILING	EQUIP	EQUIPMENT	PROJ	PROJECTOR
AFF	ABOVE FINISH FLOOR	EXG	EXISTING	RF	RADIO FREQUENCY
ASC	ABOVE SUSPENDED CEILING	FLR	FLOOR	REF	REFERENCE
AP	ACCESS PANEL	FB	FLOOR BOX	REM	REMOVE
ADD	ADDENDUM	FP	FRONT PROJECTION	REV	REVISION
ALT	ALTERNATE	FUT	FUTURE	RM	ROOM
AC	ALTERNATING CURRENT	GA	GAUGE	SCH	SCHEDULE
ANSI	AMERICAN NATIONAL STANDARDS INSTITUTE	GC	GENERAL CONTRACTOR	SEC	SECTION
AUTO	AUTOMATIC	HVAC	HEATING/COOLING	SIM	SIMILAR
BS	BOTH SIDES	HD	HEAVY-DUTY	SP	SOUNDPROOF
BOT	BOTTOM	H	HEIGHT	SPK	SPEAKER
BTU	BRITISH THERMAL UNITS	HDTV	HIGH-DEFINITION TELEVISION	SPEC	SPECIFICATION
CB	CEILING JUNCTION BOX	HOR	HORIZONTAL	STD	STANDARD
CM	CENTIMETER(S)	INCL	INCLUDED	S-VHS	SUPER VHS (VIDEO FORMAT)
COL	COLUMN	IR	INFRARED	SVGA	SUPER VIDEO GRAPHIC ADAPTER
CATV	COMMUNITY ANTENNA TV	ISDN	INTEGRATED SERVICES DIGITAL	SUS	SUSPENDED
C	CONDUIT		NETWORK	SW	SWITCH
CONF	CONFERENCE	INT	INTERIOR	SYS	SYSTEM
CONST	CONSTRUCTION	J	JUNCTION BOX	TEL/COM	TELECOMMUNICATIONS
CONT	CONTINUOUS	KO	KNOCK OUT	TEL	TELEPHONE
CONTR	CONTRACTOR	LBL	LABEL	TV	TELEVISION
D	DATA	LC	LIGHT CONTROL	TD	THROW DISTANCE
dB	DECIBEL	LVC	LOW VOLTAGE CONTROL	TYP	TYPICAL
DP	DEPTH	M	METER(S)	UON	UNLESS OTHERWISE NOTED
DIAG	DIAGONAL	MFR	MANUFACTURER	VERT	VERTICAL
DIM	DIMENSION	MAX	MAXIMUM	VGA	VIDEO GRAPHIC ADAPTER
DC	DIRECT CURRENT	MECH	MECHANICAL	VTC	VIDEO TELECONFERENCING
DR	DOOR	MIN	MINIMUM	V AC	VOLTS ALTERNATING CURRENT
DWG	DRAWING	MISC	MISCELLANEOUS	V DC	VOLTS DIRECT CURRENT
ELEC	ELECTRICAL	NTSC	NATIONAL TV SYSTEM COMMITTEE	W	WALL HUNG
EC	ELECTRICAL CONTRACTOR	NR	NOISE REDUCTION	WH	WIDTH
EL	ELEVATION	NTS	NOT TO SCALE	W/O	WITHOUT
ENC	ENCLOSURE	OFE	OWNER FURNISHED EQUIPMENT		
		OH	OVERHEAD		

COMMON SCHEMATIC CONNECTOR SYMBOLS

SFP SMALL FORM-FACTOR PLUGABLE FIBER CONNECTION (NETWORK)	TOSlink DIGITAL AUDIO
RJ45 JACK (NETWORK)	S/PDIF CONNECTOR- DIGITAL AUDIO
RJ11 JACK (TELEPHONE)	FEMALE RCA CONNECTOR
DIGITAL MEDIA CONNECTOR	1/8" MINI STEREO JACK
HDMI CONNECTOR	1/8" MINI MONO JACK
DVI CONNECTOR	1/8" TIP RING RING SLEEVE
DISPLAYPORT	PHOENIX CONNECTOR
MINI DISPLAY PORT	XLR MALE CONNECTOR (3 PIN)
VGA MALE	XLR FEMALE CONNECTOR (3 PIN)
VGA FEMALE	1/4" MALE CONNECTOR
VIDEO	1/4" FEMALE CONNECTOR
9 PIN D FEMALE	
9 PIN D MALE	
INFRARED CONNECTOR	
RF CONNECTOR	
IR, CONTROL	
USB A TYPE CONNECTOR	
USB B TYPE CONNECTOR	
USB C TYPE CONNECTOR	
MINI USB TYPE CONNECTOR	
POWER ADAPTER	

SCHEMATIC SYMBOL CONVENTIONS

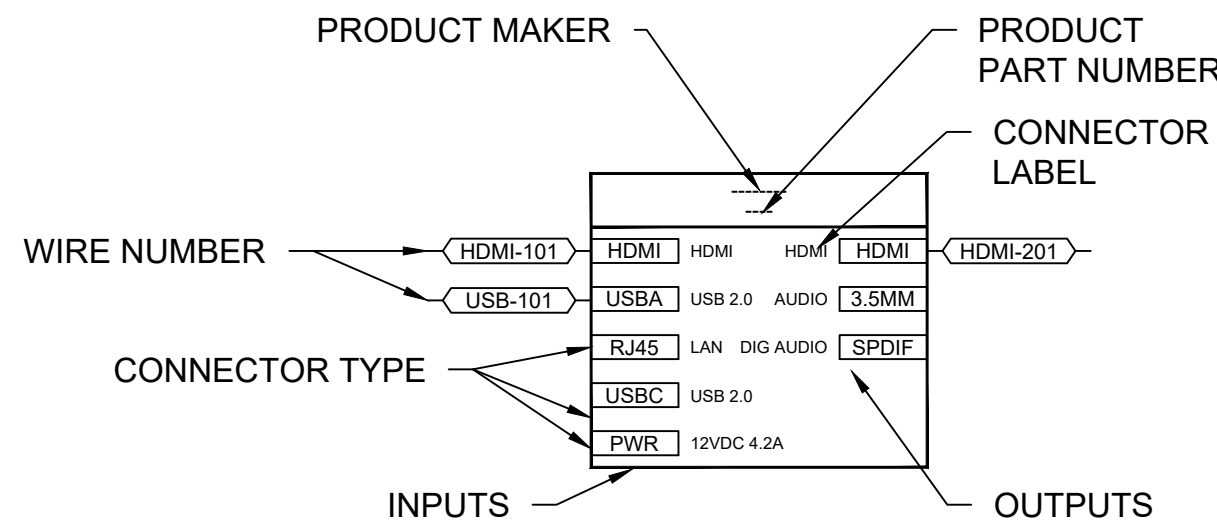

ARCHITECTURAL GENERAL INFORMATION

LCD WALL MOUNTED TOUCH PANELS

WHEN USING A WALL MOUNTED TOUCH PANELS, THE HEIGHT A.F.F. AND LOCATION MUST BE CONSIDERED FOR EASY ACCESS. TYPICAL LOCATION WILL BE NEAR THE MAIN DOOR OR IN A TRAINING ROOM SITUATION, NEAR THE PRESENTER'S DESK. TYPICAL HEIGHT A.F.F. WILL BE 54" CENTERED ON THE TOUCH PANEL.

CEILING LIFT AESTHETICS/CUSTOM TILE REQUIREMENTS

CEILING LIFTS ARE DESIGNED TO FIT IN A 2'x2' CEILING TILE. FOR A LIFT TO FIT INTO A 2'x4' CEILING TILE, IT MUST BE CENTERED IN THE TILE TO LOOK APPEALING. THE CEILING LIFT COMES WITH TRIM FOR THE LIFT TO MATCH WITH A 2'x2' TILE.

CEILING MICROPHONE CUSTOM TILE REQUIREMENTS


CEILING MICROPHONES ARE DESIGNED TO FIT IN A 2'x2' CEILING TILE. FOR A MICROPHONE TO FIT INTO A 2'x4' CEILING TILE, IT MUST BE MOUNTED IN A HARD CEILING MOUNT PROVIDED BY THE MANUFACTURE.

CEILING SPEAKERS CUSTOM TILE REQUIREMENTS

CEILING SPEAKERS ARE DESIGNED TO FIT IN A 2'x2' CEILING TILE. FOR A SPEAKER TO FIT INTO A 2'x4' CEILING SPEAKER, IT MUST BE MOUNTED IN A CUSTOM MADE TILE RAIL.

CAMERA WALL MOUNTING REQUIREMENTS

WHEN MOUNTING A CAMERA ON A WALL, THE A.F.F. HEIGHT HAS A STANDARD AS FOLLOWS. IF A CAMERA IS MOUNTED BELOW THE DISPLAY, THE CAMERA CENTER OF LENSE IS TO BE AT +48" A.F.F., AND IF A CAMERA IS MOUNTED ABOVE THE DISPLAY, THE MOUNTING HEIGHT OF THE CAMERA SHOULD BE BETWEEN 59" - 82" MOUNTING HEIGHT.

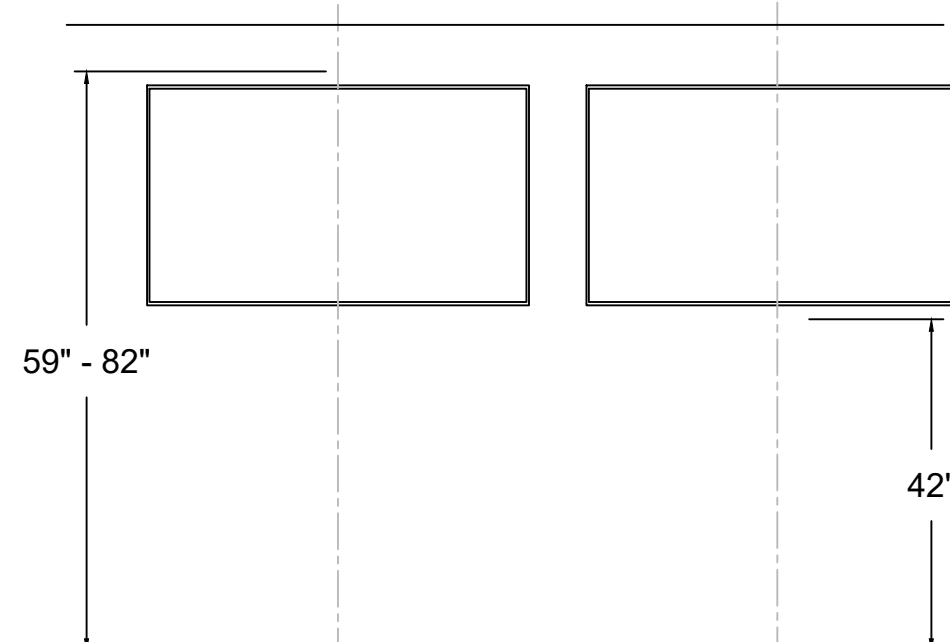

EXAMPLES

MEP GENERAL INFORMATION

AMBIENT ROOM NOISE

THE AMBIENT NOISE LEVEL IN A CONFERENCE ROOM FROM HEATING, VENTILATION, AND AIR CONDITIONING SHOULD ACHIEVE NC-25-30 NOT EXCEED NC-35. VISIONPOINT RECOMMENDS THAT THE MEASUREMENT OF THE SOUND PRESSURE LEVELS CONFORM WITH THE EQUIPMENT AND TECHNIQUES SPECIFIED IN ANSI S1.4

		Octave Band Cetrner Frequency (Hz)							
		Noise Criterion	63	125	250	500	1000	2000	4000 8000
Ideal NC	NC	NC-15	47	36	29	22	17	14	11
		NC-20	51	40	33	26	22	19	16
		NC-25	54	44	37	31	27	24	21
		NC-30	57	48	41	35	31	29	28
		NC-35	60	52	45	40	36	34	33
Acceptable NC	NC	NC-40	64	56	50	45	41	39	38
		NC-45	67	60	54	49	46	44	43
		NC-50	71	64	58	54	51	49	48
		NC-55	74	67	62	58	56	54	53
		NC-60	77	71	67	63	61	59	58
Poor Unacceptable NC	NC	NC-65	80	75	71	68	66	64	63
		NC-70	83	79	75	72	71	70	69
		NC-75	86	82	78	75	73	72	71

AMBIENT ROOM NOISE

SOUND TRANSMISSION


IN ORDER TO ACHIEVE PRIVACY AND ASSURE CONVERSATIONS IN THE CONFERENCE ROOM ARE NOT AUDIBLE OUTSIDE THE ROOM OR TO ADJACENT ROOMS A SPACE SHOULD ACHIEVE SOUND TRANSMISSION CLASS (STC) RATING OF 50 OR HIGHER. PERFORMANCE REQUIREMENTS TO MEET STC 50 ARE DETAILED IN ANSI STANDARD S12.60-202

STC	What can be heard
25	Normal speech can be understood
30	Loud speech can be understood
35	Loud speech audible but not intelligible
40	Loud speech audible as a murmur
45	Loud speech heard but not audible
50	Loud sounds faintly heard
60+	Good soundproofing; most sounds do not disturb neighbouring residents

SOUND TRANSMISSION

ACOUSTICAL PERFORMANCE

THE STANDARD RATING FOR REVERBERATION TIME IN THE CONFERENCE ROOM IS T60(SEC), AT 500HZ, 1,000HZ, AND 2,000HZ <0.3. THE SPEECH TRANSMISSION INDEX (STI) RATING IS USED FOR THE OBJECTIVE EVALUATION OF THE QUALITY OF SPEECH TRANSMISSION WITH OR WITHOUT A MICROPHONE. THE STI INDICATES TRANSMISSION QUALITY ON A SCALE FROM 0 (INCOMPREHENSIBLE) TO 1 (EXCELLENT AUDIBILITY). VISIONPOINT USES STI RATING TO CHARACTERIZE THE ACOUSTICAL PERFORMANCE OF A SPACE IN RELATION TO THE DISTANCE OF AN INDIVIDUAL TO THE MICROPHONE TECHNOLOGY. A VISIONPOINT DESIGN WILL TARGET GOOD (0.60) TO EXCELLENT (0.75) STI RATINGS. PLEASE SEE BELOW

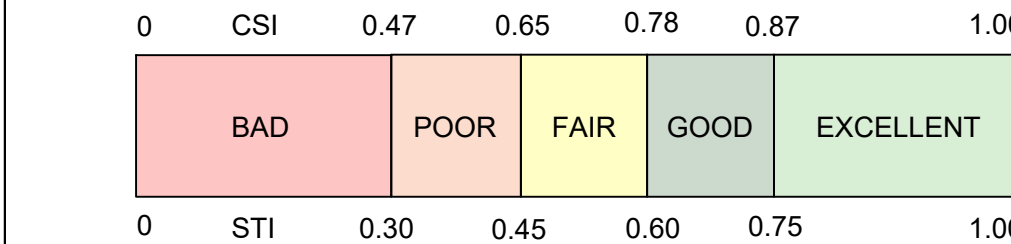

SPEECH TRANSMISSION INDEX (STI)

FURNITURE GENERAL INFORMATION

TABLE BOXES

WHEN VISIONPOINT DESIGNS A TABLE BOX THE TABLE INFORMATION NEEDS TO BE GATHERED TO INSURE THE TABLE BOX WILL WORK WITH THE FURNITURE THAT IT IS GOING INTO.

CABLE MANAGEMENT FOR FLOOR CORE AND STUB UPS


VISIONPOINT REQUIREMENTS FOR FLOOR CORES / STUB-UPS TO HAVE EITHER OF THE FOLLOWING WAYS TO CONNECT. IN THE FLOOR CORE RJ-45 CONNECTIONS FOR VISIONPOINT TO BE ABLE TO CONNECT EQUIPMENT. STUB-UPS TO BE COILED AT END SO THAT VISIONPOINT CAN TERMINATE AND DRESS CABLE FOR APPLICATIONS.

CREDENZAS

DEPENDING ON THE SIZE OF THE EQUIPMENT RACK, IT MAY BE LOCATED IN A CREDENZA PROVIDED BY THE CLIENT. WHEN THE RACK IS IN THE CREDENZA, THERE MUST BE ADEQUATE VENTILATION FOR THE RACK TO WORK PROPERLY. WHEN LOCATING EQUIPMENT INSIDE A CREDENZA OR ANY NON-CLIMATE CONTROLLED ENVIRONMENT, COORDINATE WITH THE MEP CONTRACTOR TO ENSURE THE CORRECT CALCULATION FOR AIR HANDLING. BELOW IS AN EXAMPLE FOR THE PROPER VENTILATION NEEDED FOR THE RACK:

CREDENZA FAN RECOMMENDATIONS

WHEN USING CREDENZA'S TWO FANS ARE REQUIRED SO THAT THEY HAVE PROPER VENTILATION. ONE FAN IS MOUNTED TO THE BACK OF THE CREDENZA AT THE TOP. THIS FAN WILL PUSH OUT THE HOT AIR. THE SECOND FAN IS MOUNTED TO THE BACK OF THE CREDENZA AT THE BOTTOM. THIS WILL PUSH IN COOL AIR THROUGH THE RACK

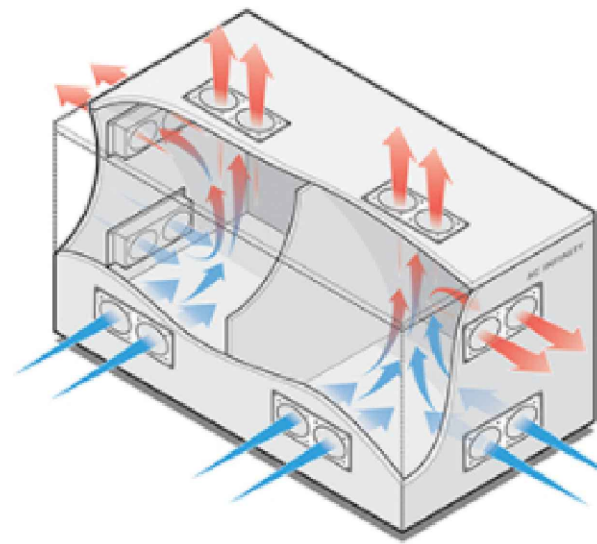

CREDENZA AIR FLOW DETAIL
(PHOTO PROVIDED BY AC INFINITY)

DRAWING LEGEND

WALL LEGEND

- J-BOX
- SENSOR J-BOX
- WALL DATA OUTLET
- WALL TELEPHONE OUTLET
- WALL TEL/DATA OUTLET
- WALL DUPLEX OUTLET
- WALL QUAD OUTLET
- RECESSED DUPLEX OUTLET
- WALL CLOCK RECEPTACLE

- M# TABLE MICROPHONE
- SAT DROP
- CATV DROP

AV-AXX WALL ELEVATION CALLOUT

AV PROJECTOR / LCD ELEVATION CALLOUT

FLOOR LEGEND

- FB# FLOOR BOX
- FLOOR DUPLEX OUTLET
- FLOOR QUAD OUTLET
- FLOOR DATA OUTLET
- FLOOR TELEPHONE OUTLET
- FLOOR TEL/DATA OUTLET

DETAIL NUMBER
 VISIONPOINT DETAIL CALLOUT
 PAGE NUMBER



















CEILING LEGEND

- LVC LOW VOLTAGE CONTROL
- P# CEILING PROJECTOR
- M1 CEILING MICROPHONE
- A# CEILING ANTENNA
- W# WIRELESS NETWORK DEVICE
- C# CEILING CAMERA
- S# CEILING SPEAKER
- E# CEILING EMITTER
- CEILING DUPLEX OUTLET
- CEILING QUAD OUTLET
- CEILING DATA OUTLET
- CEILING TELEPHONE OUTLET
- CEILING TEL/DATA OUTLET







DRAWING

AV-T1.1

COMMON CONNECTOR / RECEPTACLE TERMINATION STANDARDS

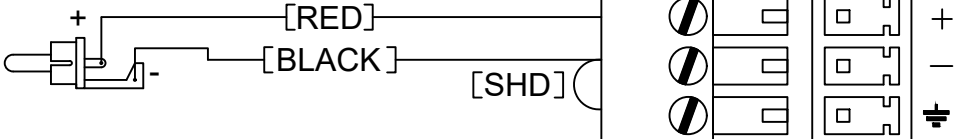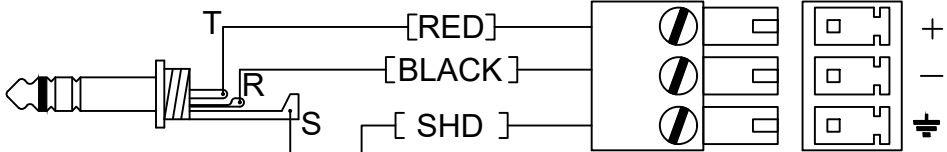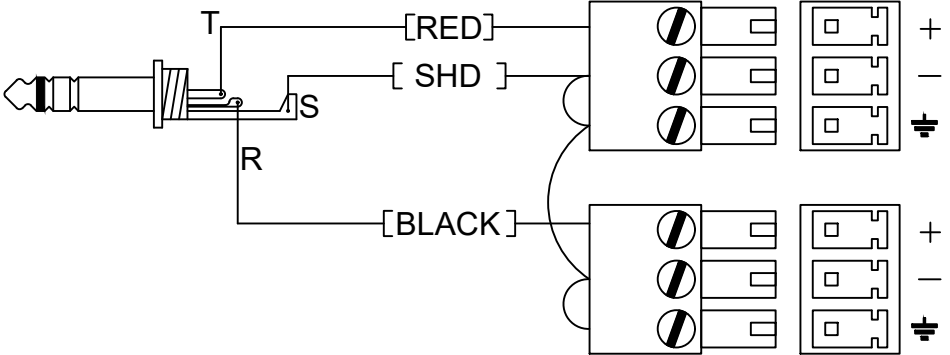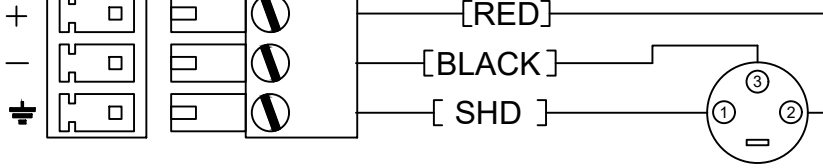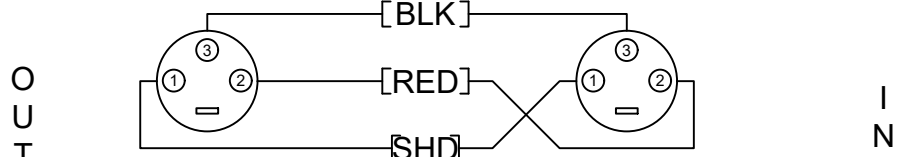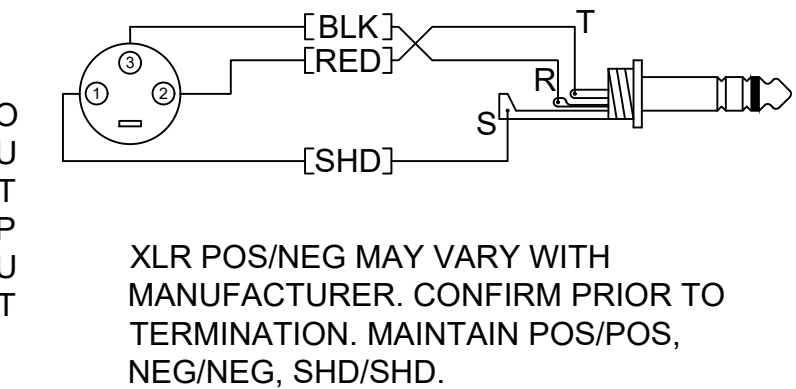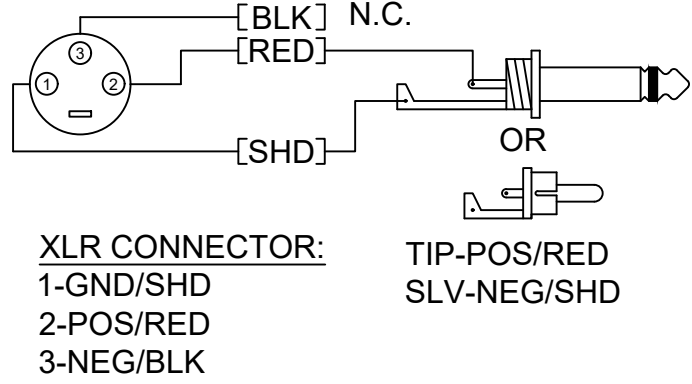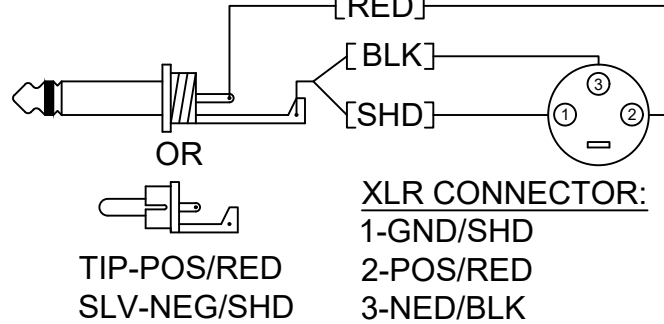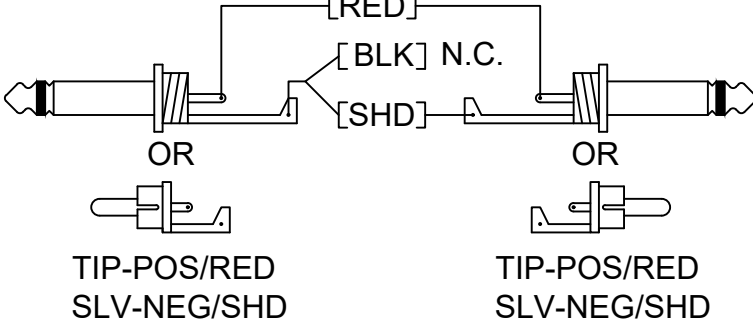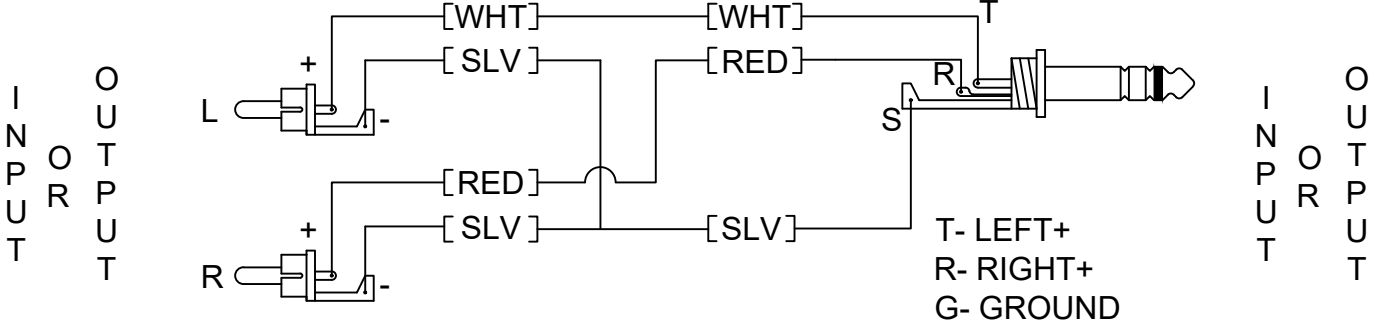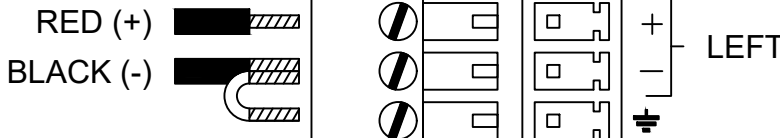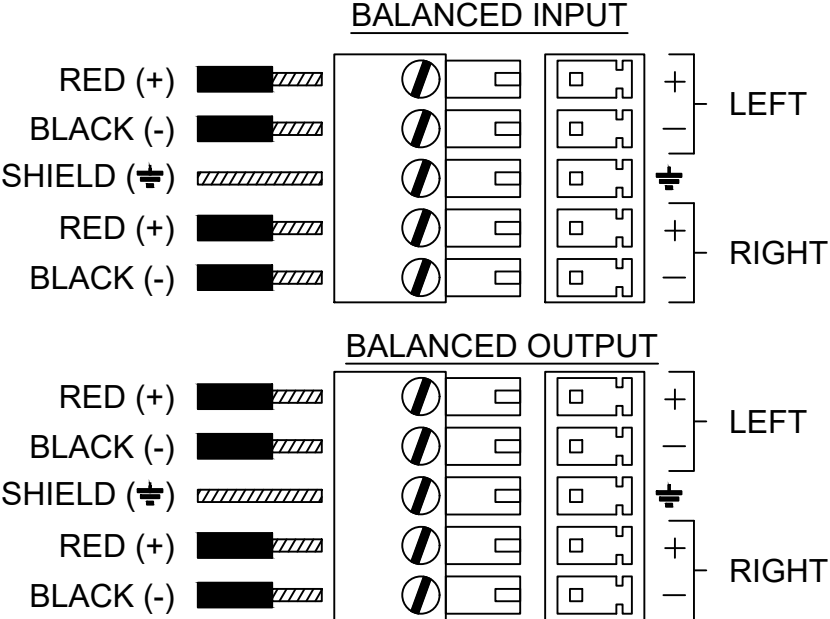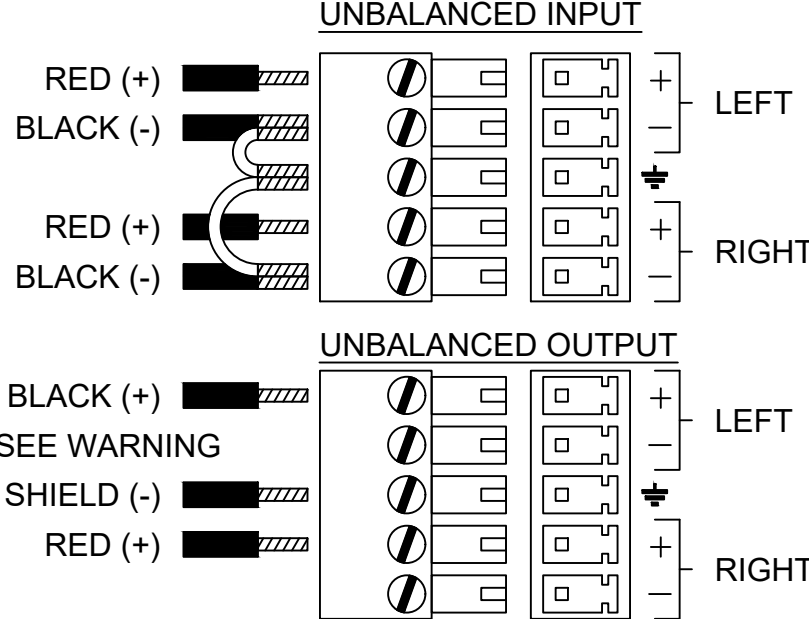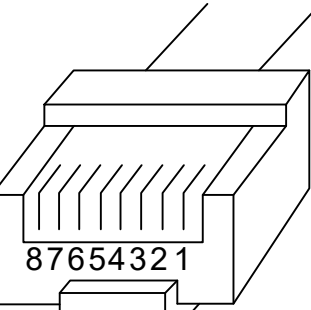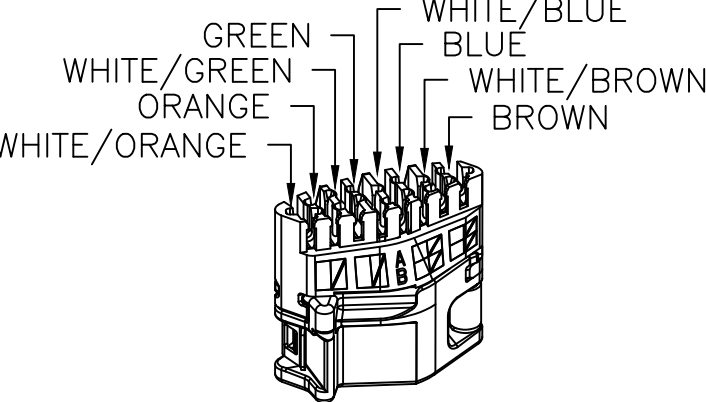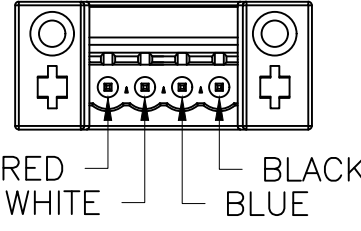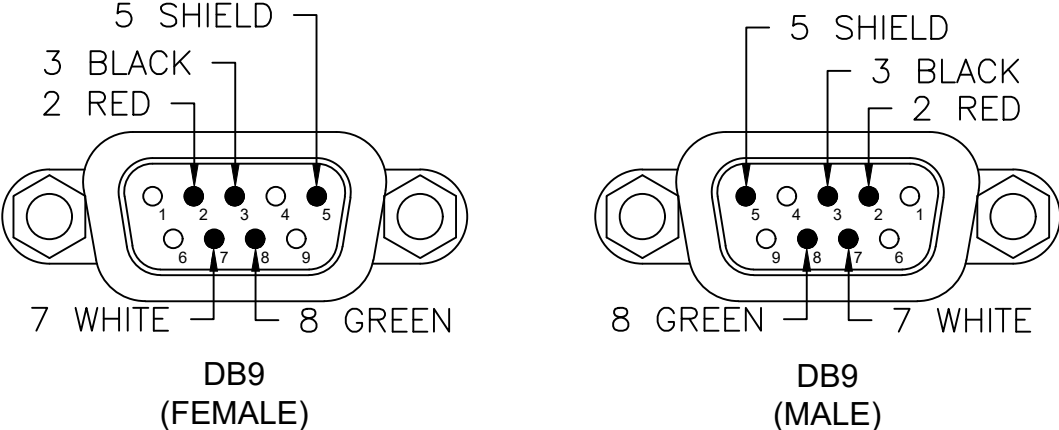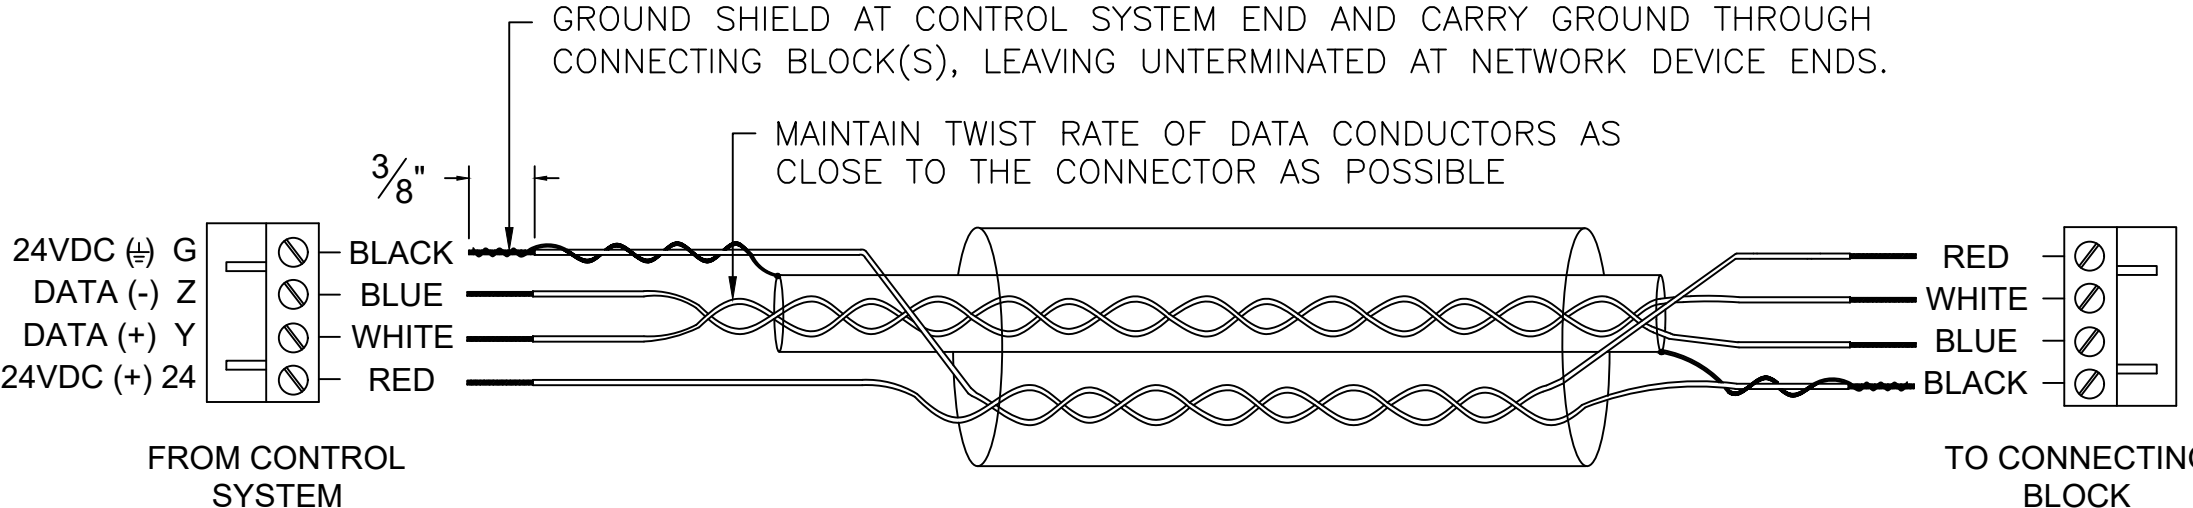RCA TO TERMINAL BLOCK (FALSE GROUND)		TRS (3.5MM) TO TERMINAL BLOCK	TRS (3.5MM) TO TERMINAL BLOCK UN-BALANCED LINE INPUT	TERMINAL BLOCK TO XLR	BALANCED-OUT TO BALANCED-IN - XLR (REAR) TO XLR
					 POS/NEG MAY VARY WITH MANUFACTURER. CONFIRM PRIOR TO TERMINATION. MAINTAIN POS/POS, NEG/NEG, SHD/SHD.
BALANCED-OUT TO BALANCED-IN - XLR (REAR) TO TRS		BALANCED-OUT TO UN-BALANCED-IN - XLR (REAR) TO RCA OR TS	UN-BALANCED-OUT TO BALANCED-IN - RCA/TS TO XLR(REAR)		UN-BALANCED-OUT TO UN-BALANCED-IN - RCA/TS TO RCA/TS
 XLR POS/NEG MAY VARY WITH MANUFACTURER. CONFIRM PRIOR TO TERMINATION. MAINTAIN POS/POS, NEG/NEG, SHD/SHD.		 XLR CONNECTOR: 1-GND/SHD 2-POS/RED 3-NEG/BLK TIP-POS/RED SLV-NEG/SHD	 XLR CONNECTOR: 1-GND/SHD 2-POS/RED 3-NEG/BLK		 TIP-POS/RED SLV-NEG/SHD
STEREO AUDIO -1/8"S TO DUAL RCA		STEREO AUDIO - UN-BALANCED WIRING		EXTRON BALANCED AUDIO WIRING	EXTRON UN-BALANCED AUDIO WIRING
				 NOTE: COLOR CODE INDICATED NOT RELEVANT FOR ALL CABLES.	 WARNING: CONNECT THE BLACK LEADS TO GROUND. CONNECTING THE BLACK LEADS TO (-) WILL DAMAGE THE AUDIO OUTPUT CIRCUITS
RJ45 WIRING	SIEMON CAT6A WIRING	CNT / PHX WIRING	DB9 WIRING	CRESNET WIRING	
 1 - WHITE/ORANGE 2 - ORANGE 3 - WHITE/GREEN 4 - BLUE 5 - WHITE/BLUE 6 - GREEN 7 - WHITE/BROWN 8 - BROWN RJ45	 SIEMON CAT6A SHIELDED CONNECTOR (CABLE CLIP ON TOP)	 CNT PHX CONNECTION	 DB9 (FEMALE) DB9 (MALE)	 WARNING: DO NOT CONNECT THE RED POWER CONDUCTOR IF ADDITIONAL POWER IS USED ON THE NEXT CONNECTING BLOCK. STRIP 1/4" OF INSULATION ON ALL CABLE ENDS THAT TERMINATE AT PHOENIX CONNECTOR TO ENSURE PROPER TERMINATION. COLOR CODE INDICATED FOR USE WITH LIBERTY PART# CRESNET (TEAL).	

ELECTRICAL LEGEND KEY

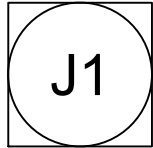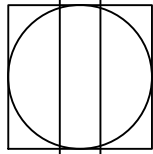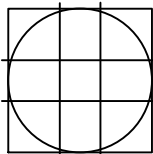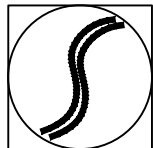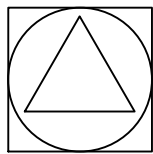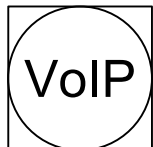LOW VOLTAGE AV BOX	
DUPLEX POWER OUTLET	
QUAD POWER OUTLET	
POWER WHIP	
DATA DROP	
CATV DROP	
VoIP DROP	

NOTES:
AT RACK LOCATION NEED AT LEAST 10'-12' EXCESS CABLE (CUT 10"-12" CABLE COVER OFF).
AT FLOOR BOXES: NEED AT LEAST 72" EXCESS CABLE.
IF A WALL PLATE APPLIES: NEED AT LEAST 36" EXCESS CABLE. ALL WALL BOXES WILL BE MUD RINGS.

CONDUIT RISER NOTES

NOTES:


1. ALL CONDUITS TO BE 1-1/4" DIAMETER UNLESS OTHERWISE SPECIFIED.
2. ELECTRICAL CONTRACTOR TO LEAVE PULL STRING IN ALL FLOOR AND WALL CONDUITS AFTER CABLE INSTALL.
3. THIS DRAWING INDICATES JUNCTION BOX NUMBERS, CABLE NUMBERS, AND CONDUIT INTERCONNECT ONLY.
4. FOR FURTHER INFORMATION, REFER TO ARCHITECTURAL AND ELECTRICAL PRINTS.
5. ALL AV INDICATES 120 VAC SERVICE LOCATIONS/OUTLETS TO BE PROVIDED WITH ISOLATED GROUNDS.
6. 120 VAC SERVICES FOR EQUIPMENT RACKS, PROJECTOR, TO SHARE SAME PHASE.
7. EC TO PROVIDE ALL CONDUITS AND JUNCTION BOXES AS INDICATED.
8. NO ELECTRICAL CONDUITS OR DEDICATED NETWORK ARE SHOWN. ONLY AV LOW VOLTAGE CONDUITS ARE INDICATED.
9. CABLE NUMBERS INDICATED ARE FOR AV LOW VOLTAGE ONLY - TEL/DATA ELECTRICAL SPECIFIED BY OTHERS.

KEY:

PLENUM BUNDLE=



STUBBED CONDUIT=

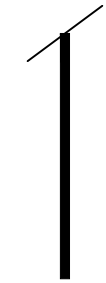

CONDUIT=



EXISTING CONDUIT=



CABLE TYPE

CODE:	DESCRIPTION:	CABLE FUNCTION:	PLENUM:	MANUFACTURER:	PART #:	COLOR:	O.D.
CAT	23-4P UNS SOL CMP C6 PURPLE JACKET	NETWORK / AUDIO / VIDEO	YES	WINDY CITY WIRE	566050	PURPLE	0.215"
CNT	18-1P+22-1P OAS CMP TEAL-YLW	CONTROL-RS-232/RELAY/IR	YES	WINDY CITY WIRE	CRESCOMP	TEAL	0.217"
SC	16-2C STR BC FRPVC FRPVC JKT WHT CMP/FPLP 75C	SPEAKER / POWER	YES	ANIXTER	AL-1602C-2-2N-01-BX	WHITE	0.198"
LLC	2-22 AWG STRANDED TINNED COPPER CONDUCTORS W/ POLYPROPYLENE INSULATION	AUDIO	YES	BELDEN	1266A 010U1000	BLACK	0.143"
DXT	2-22 AWG 2 BARE COPPER, INDIVIDUALLY SHIELDED PLENUM	AUDIO - CONTROL	YES	WINDY CITY WIRE	150100	WHITE	0.266"

COMPANY
NEWTOWN
COMMUNITY CENTER

8 SIMPSON ST,
NEWTOWN, CT 06470

ARCHITECT

N/A

CONSULTANT

N/A

PREPARED & DESIGNED BY


VISIONPOINT
Bringing People Together to Work
152 Rockwell Rd, B6,
Newington, CT 06111
Phone: (860) 436-9673
Fax: (860) 436-9790

SEAL

NOT FOR
CONSTRUCTION

STATUS
☐ PROPOSAL
☐ SKETCH
☒ PRELIMINARY
☐ REFERENCE
☐ PROGRAMMING PHASE
☐ SCHEMATIC DESIGN PHASE
☐ DESIGN DEVELOPMENT PHASE
☐ CONSTRUCTION DOCUMENTS PHASE
☐ INTEGRATION
☐ AS BUILT

PROJECT INFORMATION
PROJECT NAME: NEWTOWN
COMMUNITY CENTER
PROJECT NUMBER: P1579
PROJECT START DATE: 08/05/2026
ENGINEERED BY: KR
DRAWN BY: AVDL
SALES: MO
PROJECT MANAGER: GA
CHECKED BY: DD & MG
SCALE: NONE

LEGAL NOTICE
COPYRIGHT 2026, VISIONPOINT LLC
ALL DRAWINGS AND WRITTEN MATERIAL
HEREIN CONSTITUTE ORIGINAL AND
UNPUBLISHED WORK OF THE ENGINEER.
WRITTEN DIMENSIONS ON DRAWINGS
SHALL HAVE PRECEDENCE OVER SCALED
DIMENSIONS. CONTRACTORS SHALL
VERIFY AND BE RESPONSIBLE FOR
DIMENSIONS. VISIONPOINT LLC MUST BE
NOTIFIED OF ANY DEVIATIONS FROM
DIMENSIONS OR CONDITIONS OF SAID
DRAWINGS. SHOP DRAWINGS MUST BE
SUBMITTED FOR APPROVAL BEFORE
PROCEEDING.

STAMP

DATE:
BY:
This review is only for general conformance
with the design concept of the project and
general compliance with the information given
in the contract documents. Contractor is
responsible for dimension to be confirmed and
consistent in the details. Information that
pertains solely to the fabrication processes or
to the means, methods, techniques,
sequences, and procedures of construction;
coordination of the of all trades; and for
performing all work in a safe and satisfactory
manner.


REVISION NUMBER
REVISION #1: XXXXX/XXXX
REVISION #2: XXXXX/XXXX
REVISION #3: XXXXX/XXXX
REVISION #4: XXXXX/XXXX
REVISION #5: XXXXX/XXXX
REVISION #6: XXXXX/XXXX

RELEASE DATE
08/05/2026

TITLE
RISER AND CABLE PULL
NOTES

DRAWING
AV-T1.3

						COMPANY NEWTOWN COMMUNITY CENTER 8 SIMPSON ST, NEWTOWN, CT 06470 ARCHITECT N/A CONSULTANT N/A PREPARED & DESIGNED BY  VISIONPOINT Bringing People Together to Work 152 Rockwell Rd. B6, Newington, CT 06111 Phone: (860) 436-9673 Fax: (860) 436-9790 SEAL NOT FOR CONSTRUCTION STATUS ☐ PROPOSAL ☐ SKETCH ☒ PRELIMINARY ☐ REFERENCE ☐ PROGRAMMING PHASE ☐ SCHEMATIC DESIGN PHASE ☐ DESIGN DEVELOPMENT PHASE ☐ CONSTRUCTION DOCUMENTS PHASE ☐ INTEGRATION ☐ AS BUILT PROJECT INFORMATION PROJECT NAME: NEWTOWN COMMUNITY CENTER PROJECT NUMBER: P1573 PROJECT START DATE: 08/05/2026 ENGINEERED BY: KR DRAWN BY: AVDL SALES: MO PROJECT MANAGER: GA CHECKED BY: DD & MO SCALE: NONE LEGAL NOTICE COPYRIGHT 2026, VISIONPOINT LLC ALL DRAWINGS AND WRITTEN MATERIAL HEREIN CONSTITUTE ORIGINAL AND UNPUBLISHED WORK OF THE ENGINEER. WRITTEN DIMENSIONS ON DRAWINGS SHALL HAVE PRECEDENCE OVER SCALED DIMENSIONS. CONTRACTORS SHALL VERIFY AND BE RESPONSIBLE FOR DIMENSIONS. VISIONPOINT LLC MUST BE NOTIFIED OF ANY DEVIATIONS FROM DIMENSIONS OR CONDITIONS OF SAID DRAWINGS. SHOP DRAWINGS MUST BE SUBMITTED FOR APPROVAL BEFORE PROCEEDING. STAMP DATE: BY: The review is only for general conformance with the design concept of the project and general compliance with the information given in the contract documents. Contractor is responsible for attention to be confirmed and conformed at the jobsite. Information that pertains solely to the fabrication processes or to the means, methods, techniques, sequences, and procedures of construction; coordination of the of all trades; and for performing all work in a safe and satisfactory manner. REVISION NUMBER REVISION #1: XXX/XX/XXXX REVISION #2: XX/XX/XXXX REVISION #3: XX/XX/XXXX REVISION #4: XXX/XX/XXXX REVISION #5: XX/XX/XXXX REVISION #6: XX/XX/XXXX RELEASE DATE 08/05/2026 TITLE JOB LOCATION LAN CONNECTION SCHEDULE DRAWING AV-L1.1															
A/V LOCATION LAN CONNECTION SCHEDULE <table><tr><th>ORIGIN</th><th>DESTINATION FLOOR</th><th>DESTINATION ROOM</th><th>DESTINATION JUNCTION BOX</th><th>LAN CONNECTION LABEL</th><th>CONNECTED EQUIPMENT</th></tr><tr><td rowspan="3">IT 148</td><td rowspan="3">FIRST FLOOR</td><td rowspan="3">STORAGE 171</td><td rowspan="3">J1</td><td>LAN-101</td><td>CRESTRON IV-SAM-VX2-S</td></tr><tr><td>LAN-102</td><td>LOGITECH MEET COMPUTE</td></tr><tr><td>LAN-103</td><td>CRESTRON AM-3200-WF</td></tr></table> PLEASE NOTE, THE CABLING FOR THESE PULLS ARE NOT PROVIDED BY VISIONPOINT. THE CABLING SHOULD BE OUTSOURCED BY ANOTHER VENDOR. THIS INFORMATION IS TO ENSURE ALL NETWORK CONNECTIONS FOR A/V ARE PROVIDED AND IN THE CORRECT LOCATIONS						ORIGIN	DESTINATION FLOOR	DESTINATION ROOM	DESTINATION JUNCTION BOX	LAN CONNECTION LABEL	CONNECTED EQUIPMENT	IT 148	FIRST FLOOR	STORAGE 171	J1	LAN-101	CRESTRON IV-SAM-VX2-S	LAN-102	LOGITECH MEET COMPUTE	LAN-103	CRESTRON AM-3200-WF
ORIGIN	DESTINATION FLOOR	DESTINATION ROOM	DESTINATION JUNCTION BOX	LAN CONNECTION LABEL	CONNECTED EQUIPMENT																
IT 148	FIRST FLOOR	STORAGE 171	J1	LAN-101	CRESTRON IV-SAM-VX2-S																
				LAN-102	LOGITECH MEET COMPUTE																
				LAN-103	CRESTRON AM-3200-WF																
ARCHITECTURE COLOR LEGEND: - OWNER FURNISHED EQUIPMENT WILL BE IN BLUE - EXISTING EQUIPMENT WILL BE IN GREEN - NEW EQUIPMENT WILL BE IN BLACK																					

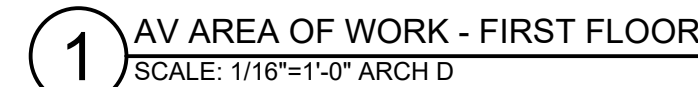

DRAWING	IND
---------	-----

AV-A0.1

A/V CABLE PULL SCHEDULE - MULTIPURPOSE 1 ROOM 165, MULTIPURPOSE 2 ROOM 167 & MULTIPURPOSE 3 ROOM 170									
FLOOR PLAN EQUIPMENT									
ORIGIN	DESTINATION		QUANTITY	CABLE	CABLE COLOR	PURPOSE	LOCATION	EXCESS CABLE BEYOND BOX	OVERALL JUNCTION BOX CABLE DIAMETER
J1 (2-GANG MUD RING)	J14	(1-GANG MUD RING)	1	CAT-101		MICROPHONE WIRELESS ACCESS POINT	WALL	36"	0.215"
	J15		1	CAT-102		BLUETOOTH WALLPLATE			
	J7		1	CAT-108					
	J8		1	CAT-109					
	J9		1	CAT-110		TOUCH PANEL			
	J10	1	CAT-124						
	J11	(2-GANG MUD RING)	1	CAT-128					
	J12		1	CAT-129					
	J2		1	CAT-117		WALLPLATE			
	J13	(1-GANG MUD RING)	1	CAT-201		TOUCH PANEL			
	J3		1	CAT-119		CAMERA			
	J4		1	CAT-120					
	J5		1	CAT-121					
	J6		1	CAT-122					
	J16		1	CAT-132		WIFI ACCESS POINT			
	J17		1	CAT-118		CAMERA			
	J18		(2-GANG MUD RING)	1	CAT-202				
CEILING EQUIPMENT									
ORIGIN	DESTINATION	DESTINATION BOX TYPE	QUANTITY	CABLE	CABLE COLOR	PURPOSE	LOCATION	EXCESS CABLE BEYOND BOX	OVERALL JUNCTION BOX CABLE DIAMETER
J1 (2-GANG MUD RING)	P1	CEILING	1	CAT-111		DECODER	CEILING	72"	0.215"
	P1		1	CAT-112		PROJECTOR			
	Z1		1	SC-501		CEILING SPEAKER LOOP			
	Z2		1	SC-502					
	Z2		1	SC-503					
	PS1		1	CNT-501		PARTITION SENSOR			0.217"
	PS2		1	CNT-502		PARTITION SENSOR			

FOR LAN / VOIP / TECLO / CATV CONNECTIONS

PLEASE SEE CONNECTIONS FOR CLIENT / CABLE PULLER RESPONSIBILITIES ON A/V-L1.1

1MULTIPURPOSE 1 ROOM 165, MULTIPURPOSE 2 ROOM 167 & MULTIPURPOSE 3 ROOM 170 - CABLE PULL SCHEDULE

SCALE: N.T.S.

ARCHITECTURE COLOR LEGEND:

- OWNER FURNISHED EQUIPMENT WILL BE IN BLUE
- EXISTING EQUIPMENT WILL BE IN GREEN
- NEW EQUIPMENT WILL BE IN BLACK

COMPANY
NEWTOWN
COMMUNITY CENTER

8 SIMPSON ST,
NEWTOWN, CT 06470

ARCHITECT

N/A

CONSULTANT

N/A

PREPARED & DESIGNED BY


VISIONPOINT
Bringing People Together to Work
152 Rockwell Rd. B6,
Newington, CT 06111
Phone: (860) 436-9673
Fax: (860) 436-9790

SEAL

NOT FOR
CONSTRUCTION

STATUS
☐ PROPOSAL
☐ SKETCH
☒ PRELIMINARY
☐ REFERENCE
☐ PROGRAMMING PHASE
☐ SCHEMATIC DESIGN PHASE
☐ DESIGN DEVELOPMENT PHASE
☐ CONSTRUCTION DOCUMENTS PHASE
☐ INTEGRATION
☐ AS BUILT

PROJECT INFORMATION
PROJECT NAME: NEWTOWN
COMMUNITY CENTER
PROJECT NUMBER: P1579
PROJECT START DATE: 08/05/2026
ENGINEERED BY: KR
DRAWN BY: AVDL
SALES: MO
PROJECT MANAGER: GA
CHECKED BY: DD & MG
SCALE: NONE

LEGAL NOTICE
COPYRIGHT 2026, VISIONPOINT LLC
ALL DRAWINGS AND WRITTEN MATERIAL
HEREIN CONSTITUTE ORIGINAL AND
UNPUBLISHED WORK OF THE ENGINEER.
WRITTEN DIMENSIONS ON DRAWINGS
SHALL HAVE PRECEDENCE OVER SCALED
DIMENSIONS. CONTRACTORS SHALL
VERIFY AND BE RESPONSIBLE FOR
DIMENSIONS. VISIONPOINT LLC MUST BE
NOTIFIED OF ANY DEVIATIONS FROM
DIMENSIONS OR CONDITIONS OF SAID
DRAWINGS. SHOP DRAWINGS MUST BE
SUBMITTED FOR APPROVAL BEFORE
PROCEEDING.

STAMP


DATE:
DL
This review is only for general conformance
with the design concept of the project and
general compliance with the information given
in the contract documents. Contractor is
responsible for dimension to be confirmed and
correlated at the jobsite. Information that
pertains solely to the fabrication processes or
to the means, methods, techniques,
sequences, and procedures of construction;
coordination of the of all trades; and for
performing all work in a safe and satisfactory
manner.

REVISION NUMBER
REVISION #1: XXXXXXXX
REVISION #2: XXXXXXXX
REVISION #3: XXXXXXXX
REVISION #4: XXXXXXXX
REVISION #5: XXXXXXXX
REVISION #6: XXXXXXXX

RELEASE DATE
08/05/2026

TITLE
MULTIPURPOSE 1 ROOM 165,
MULTIPURPOSE 2 ROOM 167
& MULTIPURPOSE 3 ROOM
170,
CABLE PULL SCHEDULE

DRAWING INDEX
AV-A1.1

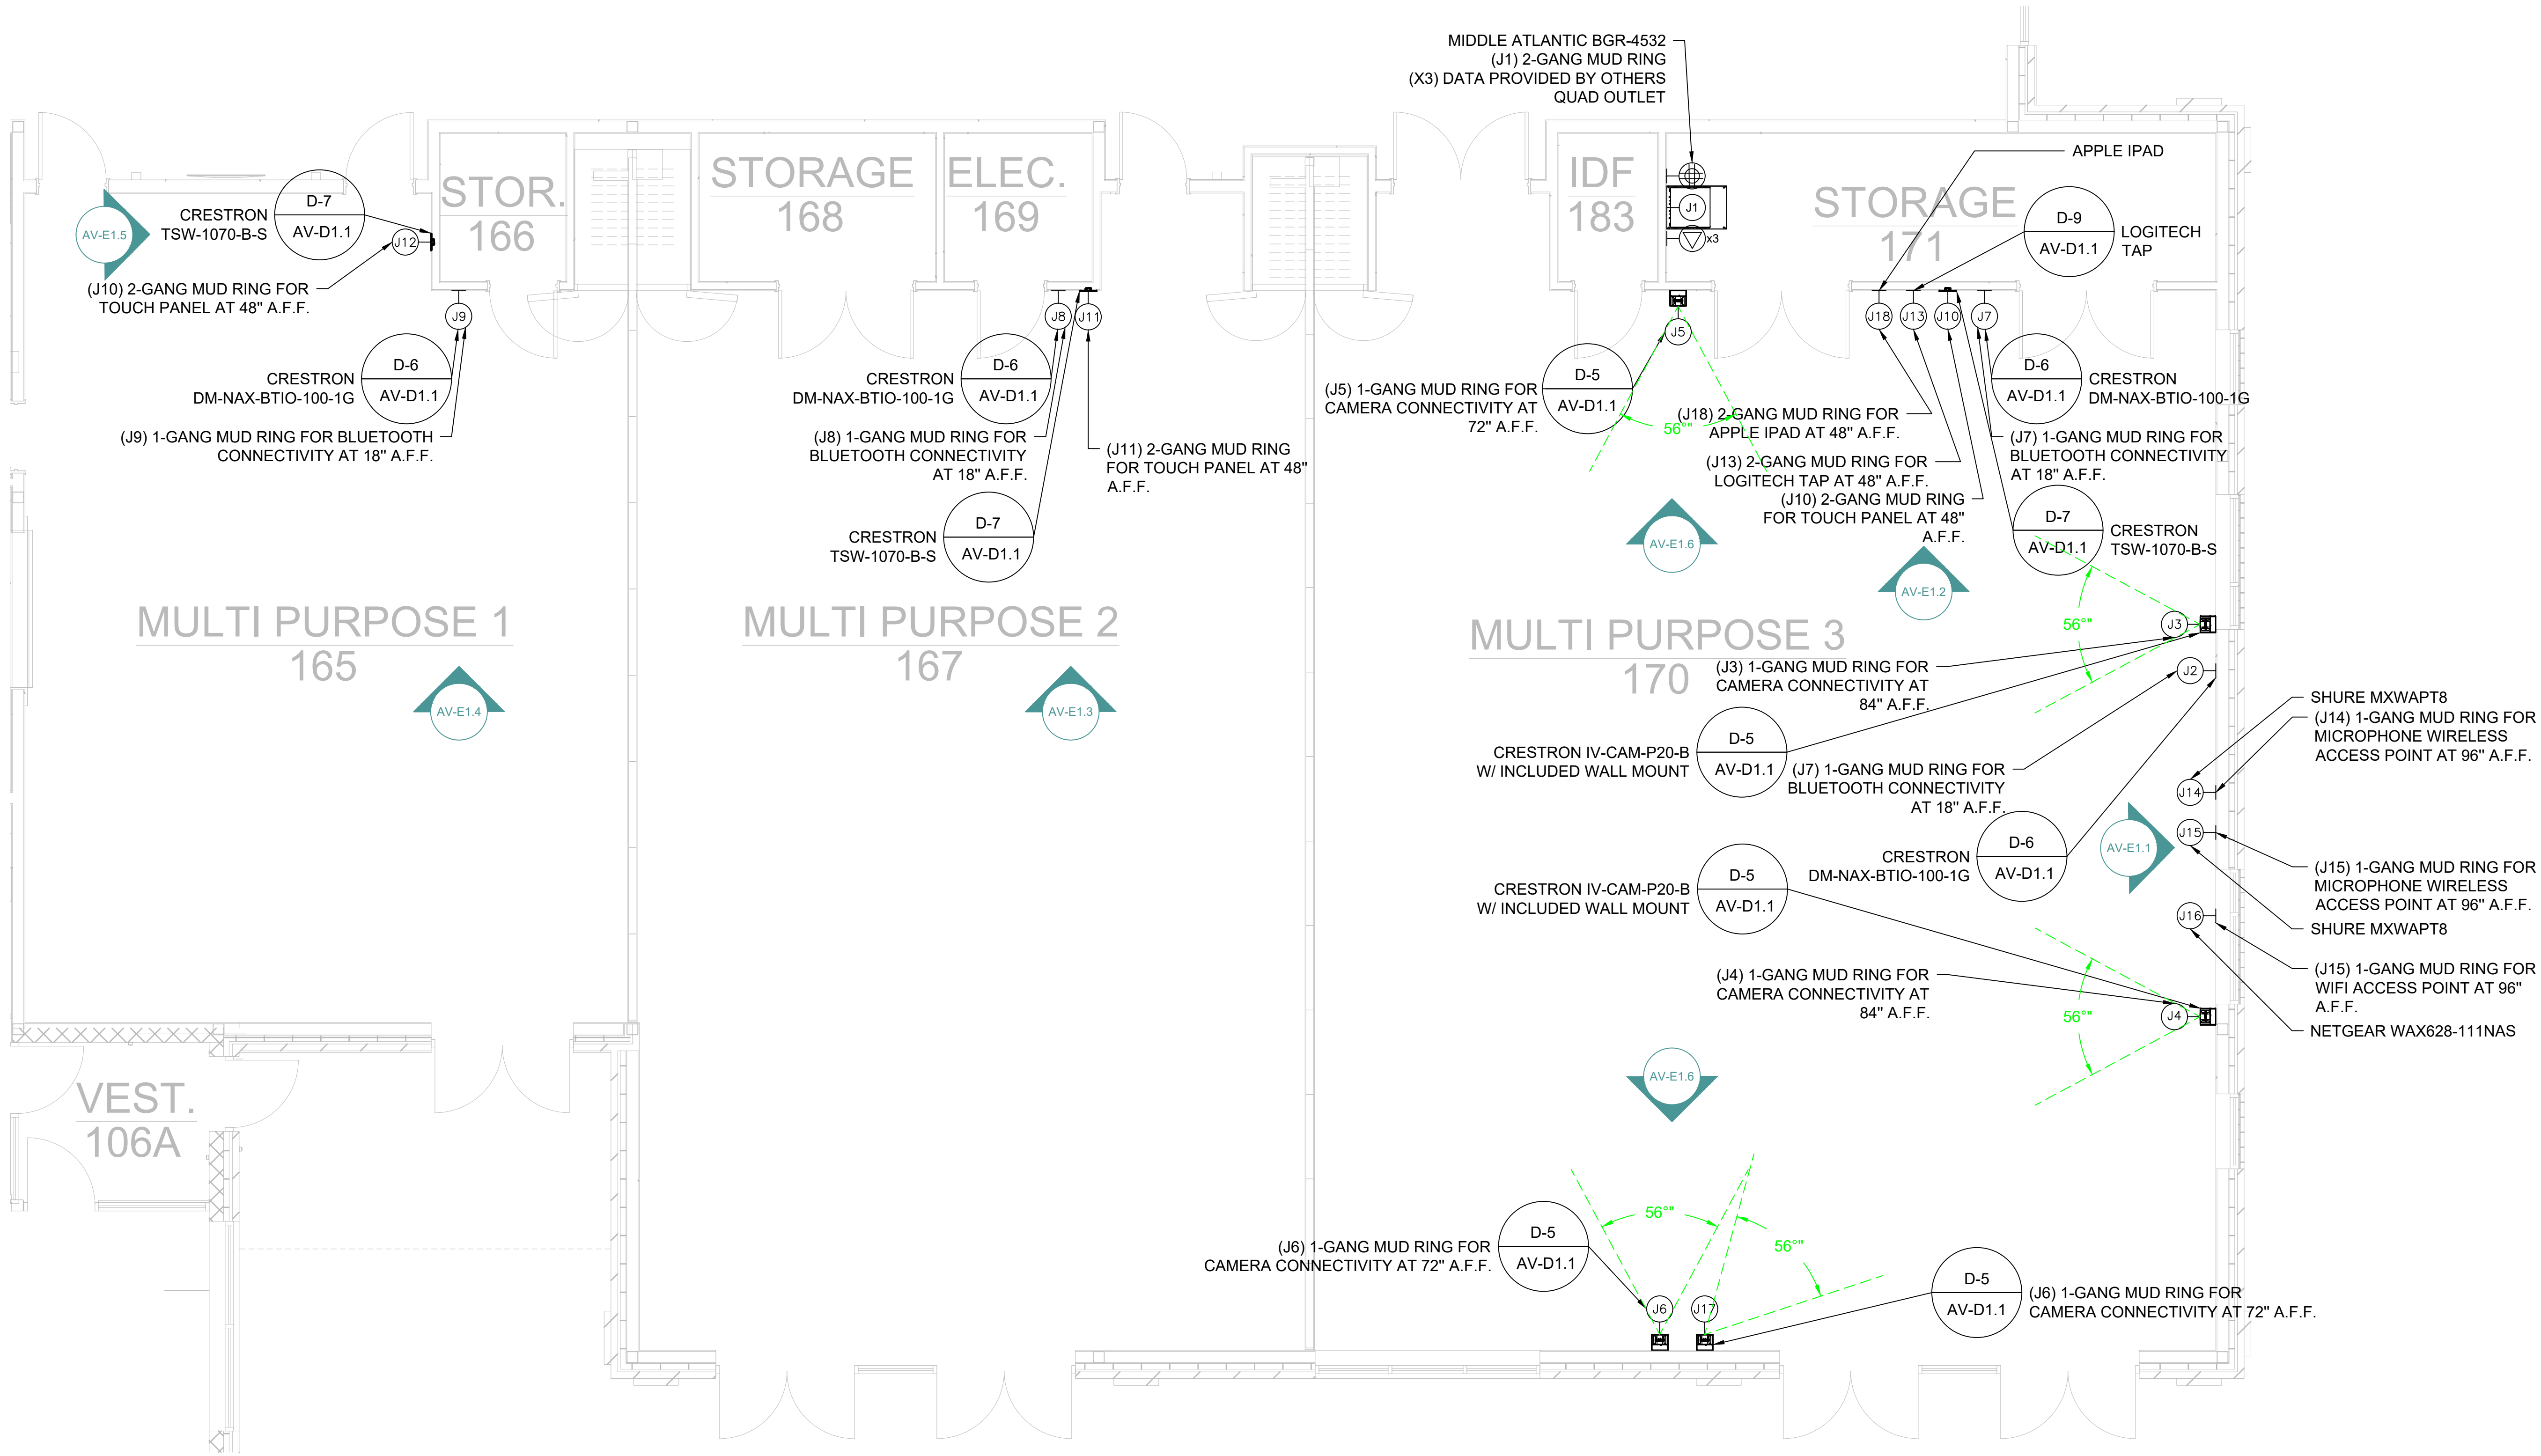

1 MULTIPURPOSE 1 ROOM 165, MULTIPURPOSE 2 ROOM 167 & MULTIPURPOSE 3 ROOM 170 - FLOOR PLAN
SCALE: 1/4"=1'-0" ARCH D

ARCHITECTURE COLOR LEGEND:
- OWNER FURNISHED EQUIPMENT WILL BE IN BLUE
- EXISTING EQUIPMENT WILL BE IN GREEN
- NEW EQUIPMENT WILL BE IN BLACK

COMPANY
NEWTOWN
COMMUNITY CENTER

8 SIMPSON ST,
NEWTOWN, CT 06470

ARCHITECT
N/A

CONSULTANT
N/A

PREPARED & DESIGNED BY

VISIONPOINT
Bringing People Together to Work
152 Rockwell Rd. B6,
Newington, CT 06111
Phone: (860) 436-9673
Fax: (860) 436-9790

SEAL
NOT FOR
CONSTRUCTION

☐ PROPOSAL
☐ SKETCH
☒ PRELIMINARY
☐ REFERENCE
☐ PROGRAMMING PHASE
☐ SCHEMATIC DESIGN PHASE
☐ DESIGN DEVELOPMENT PHASE
☐ CONSTRUCTION DOCUMENTS PHASE
☐ INTEGRATION
☐ AS BUILT

PROJECT INFORMATION
PROJECT NAME: NEWTOWN
COMMUNITY CENTER
PROJECT NUMBER: P1579
PROJECT START DATE: 08/05/2026
ENGINEERED BY: KR
DRAWN BY: AVDL
SALES: MO
PROJECT MANAGER: GA
CHECKED BY: DD & MG
SCALE: NONE

LEGAL NOTICE
COPYRIGHT 2026, VISIONPOINT LLC
ALL DRAWINGS AND WRITTEN MATERIAL
HEREIN, CONSTITUTE ORIGINAL AND
UNPUBLISHED WORK OF THE ENGINEER.
WRITTEN DIMENSIONS ON DRAWINGS
SHALL HAVE PRECEDENCE OVER SCALED
DIMENSIONS. CONTRACTORS SHALL
VERIFY AND BE RESPONSIBLE FOR
DIMENSIONS. VISIONPOINT LLC MUST BE
NOTIFIED OF ANY DEVIATIONS FROM
DIMENSIONS OR CONDITIONS OF SAID
DRAWINGS. SHOP DRAWINGS MUST BE
SUBMITTED FOR APPROVAL BEFORE
PROCEEDING.

STAMP


DATE:
DL
This review is only for general conformance
with the design concept of the project and
general compliance with the information given
in the contract documents. Contractor is
responsible for dimension to be confirmed and
corrected at the jobsite. Information that
pertains solely to the fabrication processes or
to the means, methods, techniques,
sequences, and procedures of construction;
coordination of the work of all trades; and for
performing all work in a safe and satisfactory
manner.

REVISION NUMBER
REVISION #1: XXXXXXXX
REVISION #2: XXXXXXXX
REVISION #3: XXXXXXXX
REVISION #4: XXXXXXXX
REVISION #5: XXXXXXXX
REVISION #6: XXXXXXXX

RELEASE DATE
08/05/2026

TITLE
MULTIPURPOSE 1 ROOM 165,
MULTIPURPOSE 2 ROOM 167
& MULTIPURPOSE 3 ROOM
170,
FLOOR PLAN

DRAWING INDEX
AV-A1.2

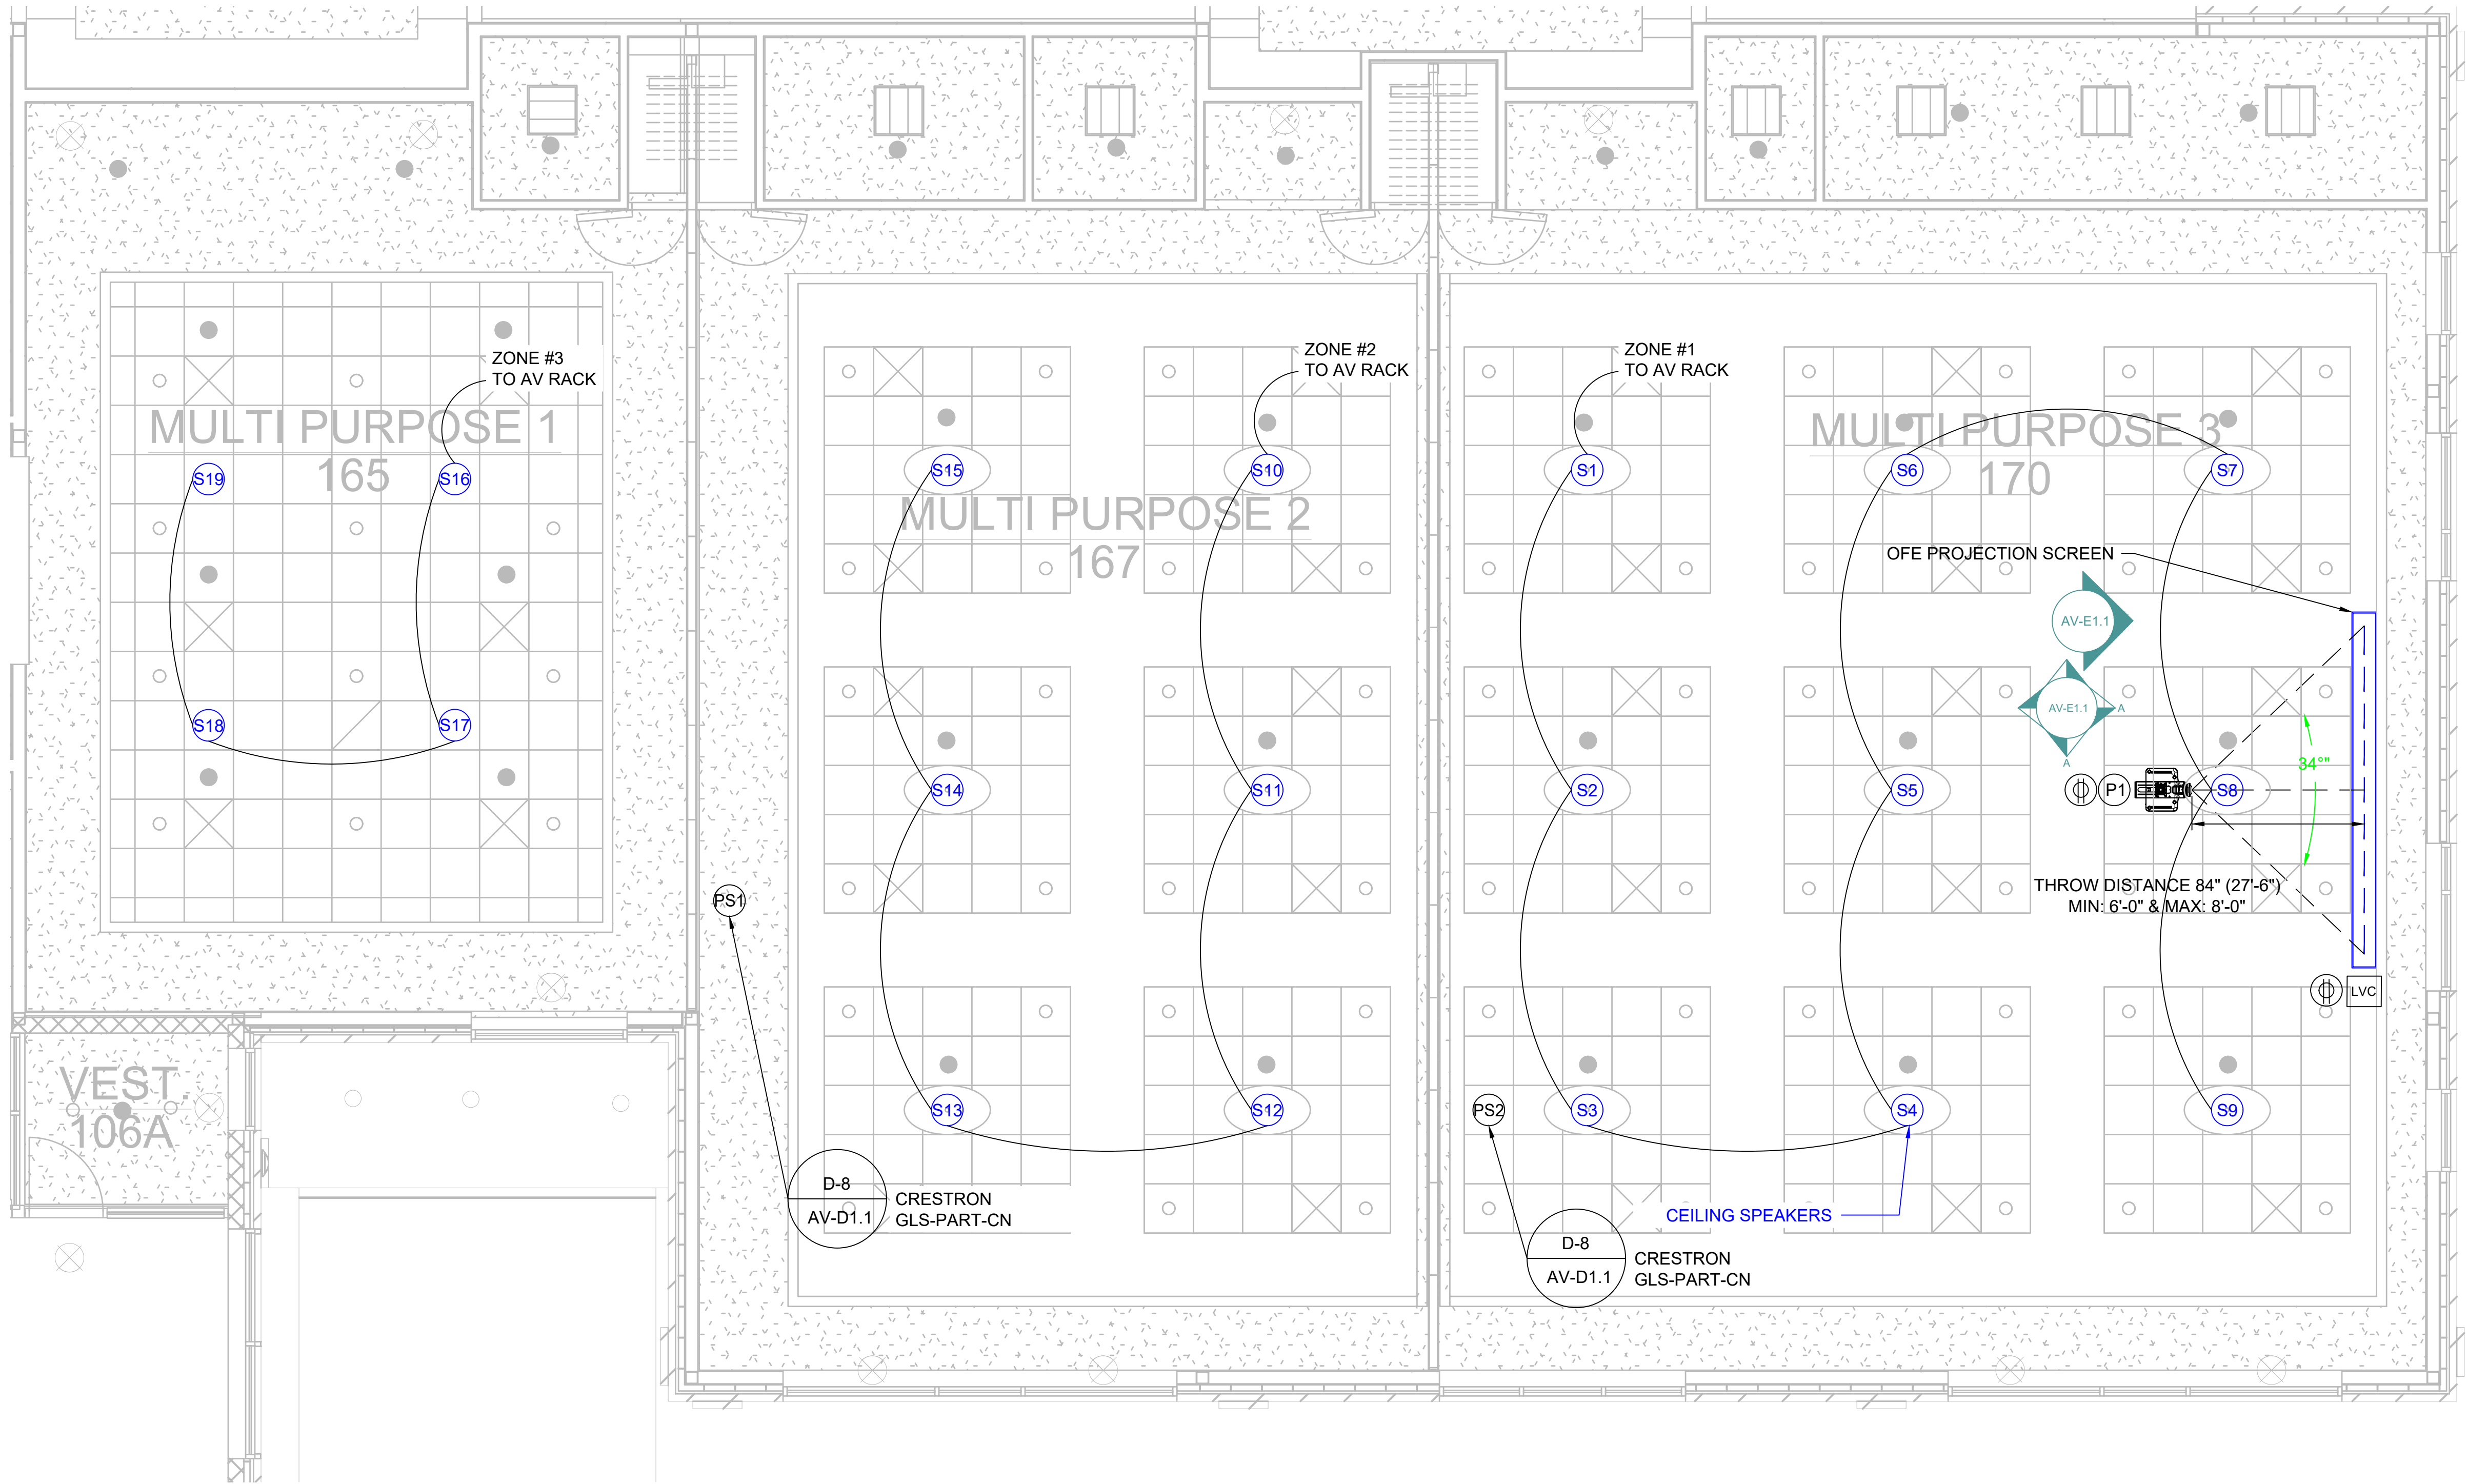

1 MULTIPURPOSE 1 ROOM 165, MULTIPURPOSE 2 ROOM 167 & MULTIPURPOSE 3 ROOM 170 - CEILING PLAN
SCALE: 1/4"=1'-0" ARCH D

ARCHITECTURE COLOR LEGEND:
- OWNER FURNISHED EQUIPMENT WILL BE IN BLUE
- EXISTING EQUIPMENT WILL BE IN GREEN
- NEW EQUIPMENT WILL BE IN BLACK

COMPANY
NEWTOWN
COMMUNITY CENTER

8 SIMPSON ST,
NEWTOWN, CT 06470

ARCHITECT
N/A

CONSULTANT
N/A

PREPARED & DESIGNED BY

VISIONPOINT
Bringing People Together to Work
152 Rockwell Rd. B6,
Newington, CT 06111
Phone: (860) 436-9673
Fax: (860) 436-9790

SEAL
NOT FOR
CONSTRUCTION

STATUS
☐ PROPOSAL
☐ SKETCH
☒ PRELIMINARY
☐ REFERENCE
☐ PROGRAMMING PHASE
☐ SCHEMATIC DESIGN PHASE
☐ DESIGN DEVELOPMENT PHASE
☐ CONSTRUCTION DOCUMENTS PHASE
☐ INTEGRATION
☐ AS BUILT

PROJECT INFORMATION
PROJECT NAME: NEWTOWN COMMUNITY CENTER
PROJECT NUMBER: P1579
PROJECT START DATE: 08/05/2026
ENGINEERED BY: KR
DRAWN BY: AVDL
SALES: MO
PROJECT MANAGER: GA
CHECKED BY: DO & MG
SCALE: NONE

LEGAL NOTICE
COPYRIGHT 2026, VISIONPOINT LLC
ALL DRAWINGS AND WRITTEN MATERIAL
HEREIN CONSTITUTE ORIGINAL AND
UNPUBLISHED WORK OF THE ENGINEER.
WRITTEN DIMENSIONS ON DRAWINGS
SHALL HAVE PRECEDENCE OVER SCALED
DIMENSIONS. CONTRACTORS SHALL
VERIFY AND BE RESPONSIBLE FOR
DIMENSIONS. VISIONPOINT LLC MUST BE
NOTIFIED OF ANY DEVIATIONS FROM
DIMENSIONS OR CONDITIONS OF SAID
DRAWINGS. SHOP DRAWINGS MUST BE
SUBMITTED FOR APPROVAL BEFORE
PROCEEDING.

STAMP

DATE:
DL
This review is only for general conformance
with the design concept of the project and
general compliance with the information given
in the contract documents. Contractor is
responsible for dimension to be confirmed and
corrected at the fabricator. Information that
pertains solely to the fabrication processes or
to the means, methods, techniques,
sequences, and procedures of construction;
coordination of the work of all trades; and for
performing all work in a safe and satisfactory
manner.

REVISION NUMBER
REVISION #1: XXXXXXXX
REVISION #2: XXXXXXXX
REVISION #3: XXXXXXXX
REVISION #4: XXXXXXXX
REVISION #5: XXXXXXXX
REVISION #6: XXXXXXXX

RELEASE DATE
08/05/2026


TITLE
MULTIPURPOSE 1 ROOM 165,
MULTIPURPOSE 2 ROOM 167
& MULTIPURPOSE 3 ROOM
170.
CEILING PLAN

DRAWING INDEX


AV-A1.3





EQUIPMENT SCHEDULE	
VIDEO PROJECTOR:	CHRISTIE 4K1000-KS
LENS:	140-166104-01 ZOOM LENS
PROJECTOR MOUNT:	CHIEF RPMAUW
IMAGE SIZE:	T.B.D.
IMAGE RATIO:	T.B.D.
MIN. THROW DISTANCE:	72" (6')
CENTER THROW:	84" (7')
MAX. THROW DISTANCE:	96" (8')
SCREEN MODEL:	OFE
PLENUM RATED	
CEILING BOX:	N/A

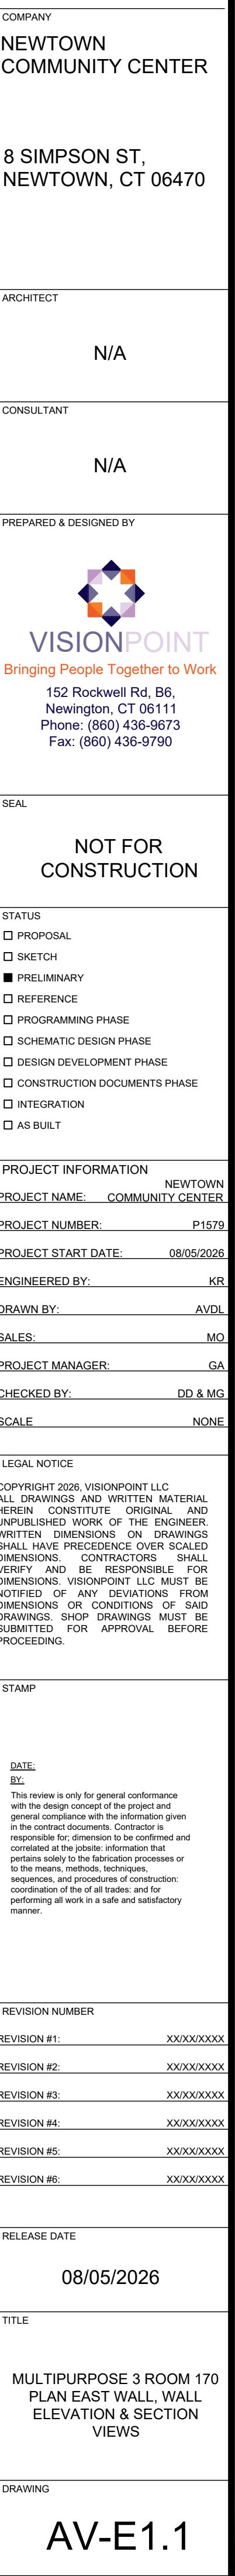

AV-E1.1

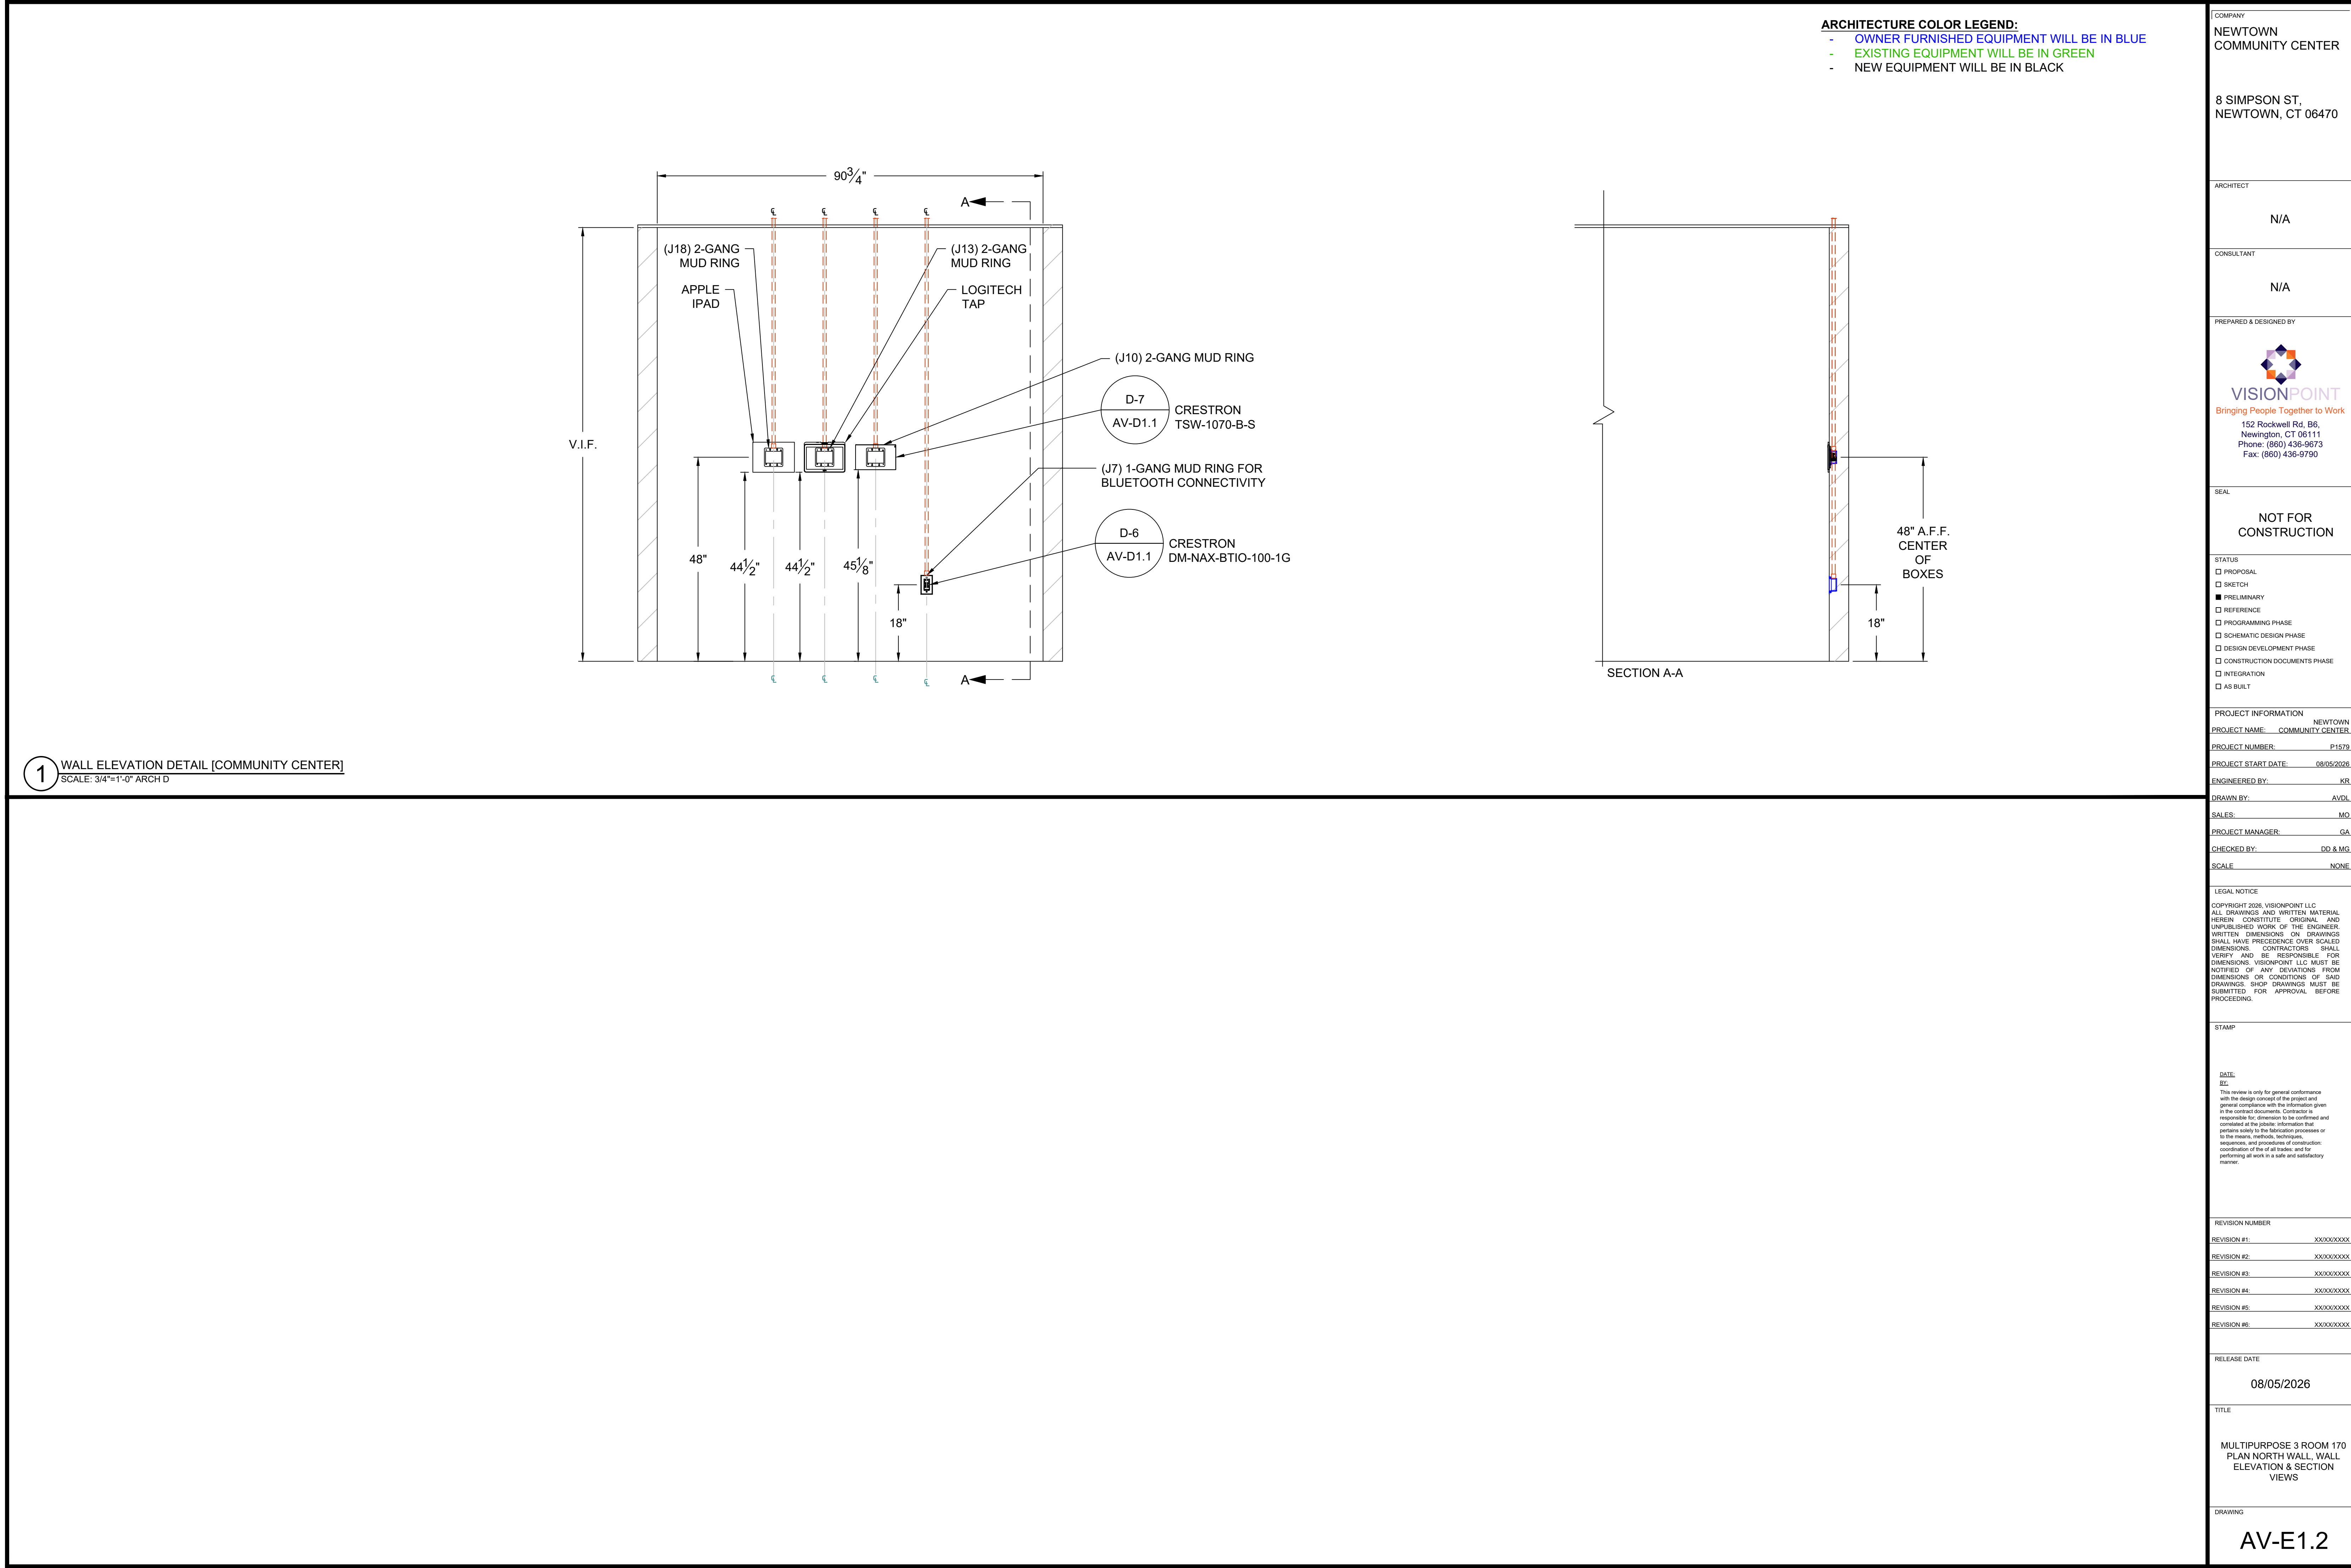

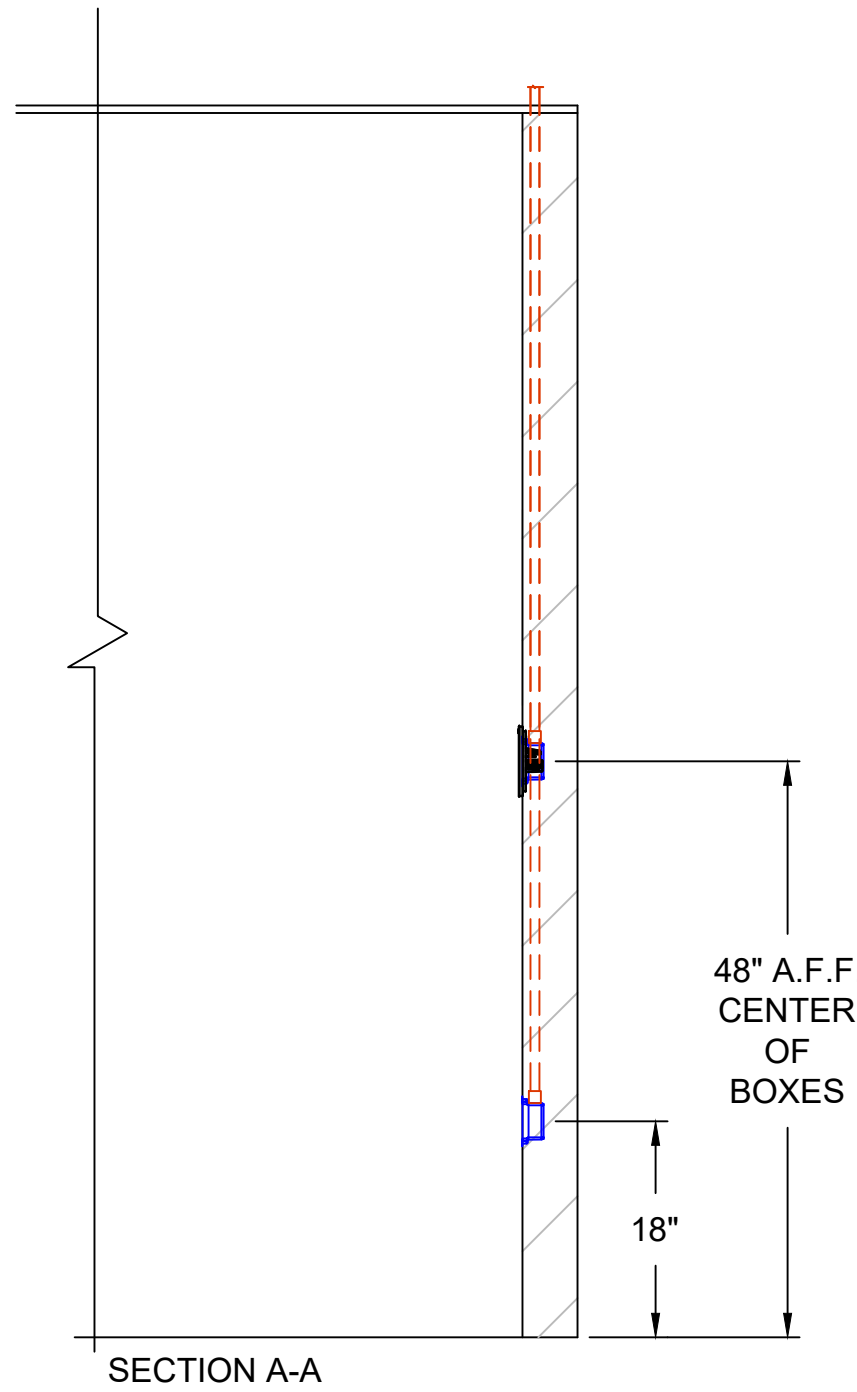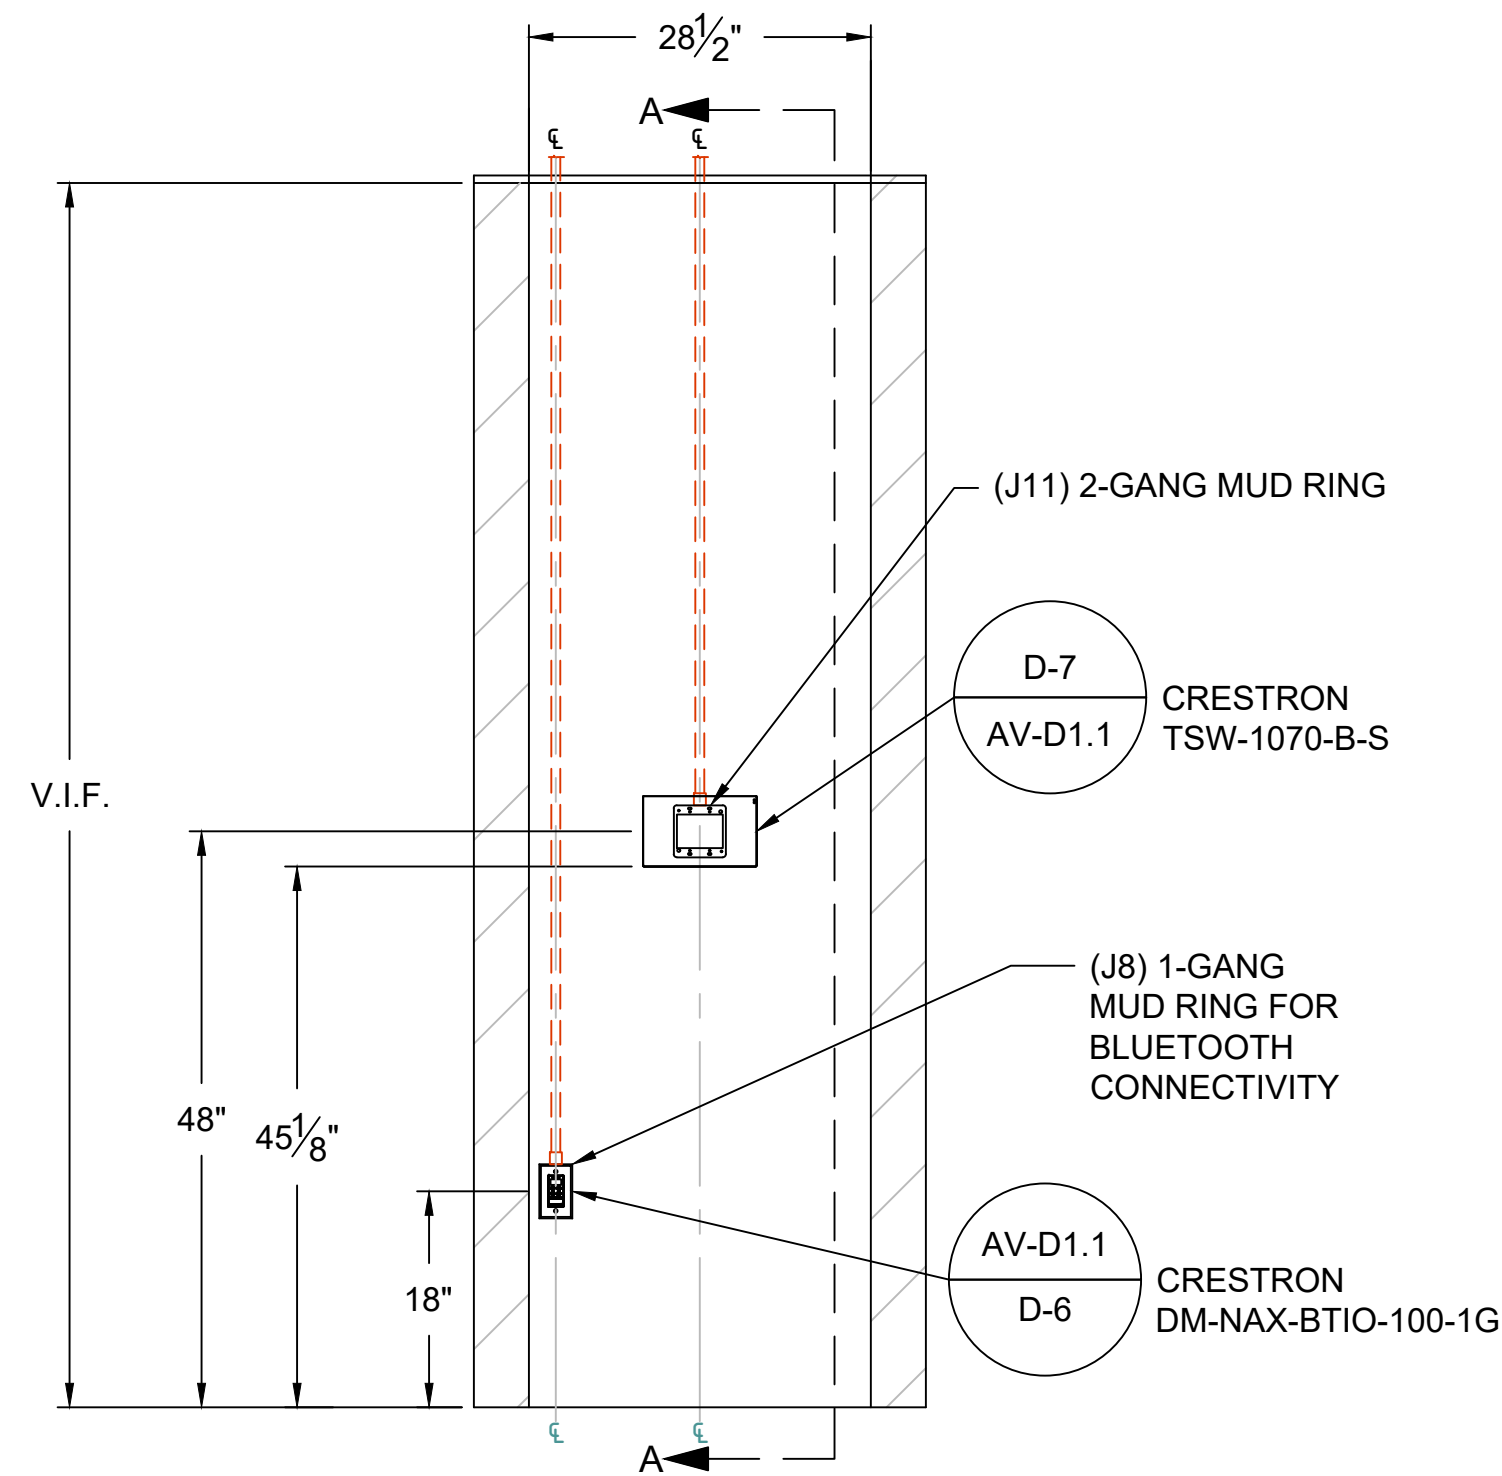

1 WALL ELEVATION DETAIL [COMMUNITY CENTER]
SCALE: 3/4"=1'-0" ARCH D

ARCHITECTURE COLOR LEGEND:
- OWNER FURNISHED EQUIPMENT WILL BE IN BLUE
- EXISTING EQUIPMENT WILL BE IN GREEN
- NEW EQUIPMENT WILL BE IN BLACK

COMPANY
NEWTOWN
COMMUNITY CENTER

8 SIMPSON ST,
NEWTOWN, CT 06470

ARCHITECT
N/A

CONSULTANT
N/A

PREPARED & DESIGNED BY

VISIONPOINT
Bringing People Together to Work
152 Rockwell Rd. B6,
Newington, CT 06111
Phone: (860) 436-9673
Fax: (860) 436-9790

SEAL
NOT FOR
CONSTRUCTION

STATUS
☐ PROPOSAL
☐ SKETCH
☒ PRELIMINARY
☐ REFERENCE
☐ PROGRAMMING PHASE
☐ SCHEMATIC DESIGN PHASE
☐ DESIGN DEVELOPMENT PHASE
☐ CONSTRUCTION DOCUMENTS PHASE
☐ INTEGRATION
☐ AS BUILT

PROJECT INFORMATION
PROJECT NAME: NEWTOWN COMMUNITY CENTER
PROJECT NUMBER: P1579
PROJECT START DATE: 08/05/2026
ENGINEERED BY: KR
DRAWN BY: AVDL
SALES: MO
PROJECT MANAGER: GA
CHECKED BY: DG & MG
SCALE: NONE

LEGAL NOTICE
COPYRIGHT 2026, VISIONPOINT LLC.
ALL DRAWINGS AND WRITTEN MATERIAL
HEREIN CONSTITUTE ORIGINAL AND
UNPUBLISHED WORK OF THE ENGINEER.
WRITTEN DIMENSIONS ON DRAWINGS
SHALL HAVE PRECEDENCE OVER SCALED
DIMENSIONS. CONTRACTORS SHALL
VERIFY AND BE RESPONSIBLE FOR
DIMENSIONS. VISIONPOINT LLC MUST BE
NOTIFIED OF ANY DEVIATIONS FROM
DIMENSIONS OR CONDITIONS OF SAID
DRAWINGS. SHOP DRAWINGS MUST BE
SUBMITTED FOR APPROVAL BEFORE
PROCEEDING.

STAMP

DATE:
BY:
This review is only for general conformance
with the design concept of the project and
general compliance with the information given
in the contract documents. Contractor is
responsible for dimension to be confirmed and
corrected at the place. Information that
pertains solely to the fabrication processes or
to the means, methods, techniques,
equipment, and procedures of construction;
coordination of the of all trades; and for
performing all work in a safe and satisfactory
manner.



REVISION NUMBER
REVISION #1: XXXXXXXXXX
REVISION #2: XXXXXXXXXX
REVISION #3: XXXXXXXXXX
REVISION #4: XXXXXXXXXX
REVISION #5: XXXXXXXXXX
REVISION #6: XXXXXXXXXX

RELEASE DATE
08/05/2026

TITLE
MULTIPURPOSE 2 ROOM 167
PLAN NORTH WALL, WALL
ELEVATION & SECTION
VIEWS

DRAWING
AV-E1.3

1 WALL ELEVATION DETAIL [COMMUNITY CENTER]
SCALE: 3/4"=1'-0" ARCH D

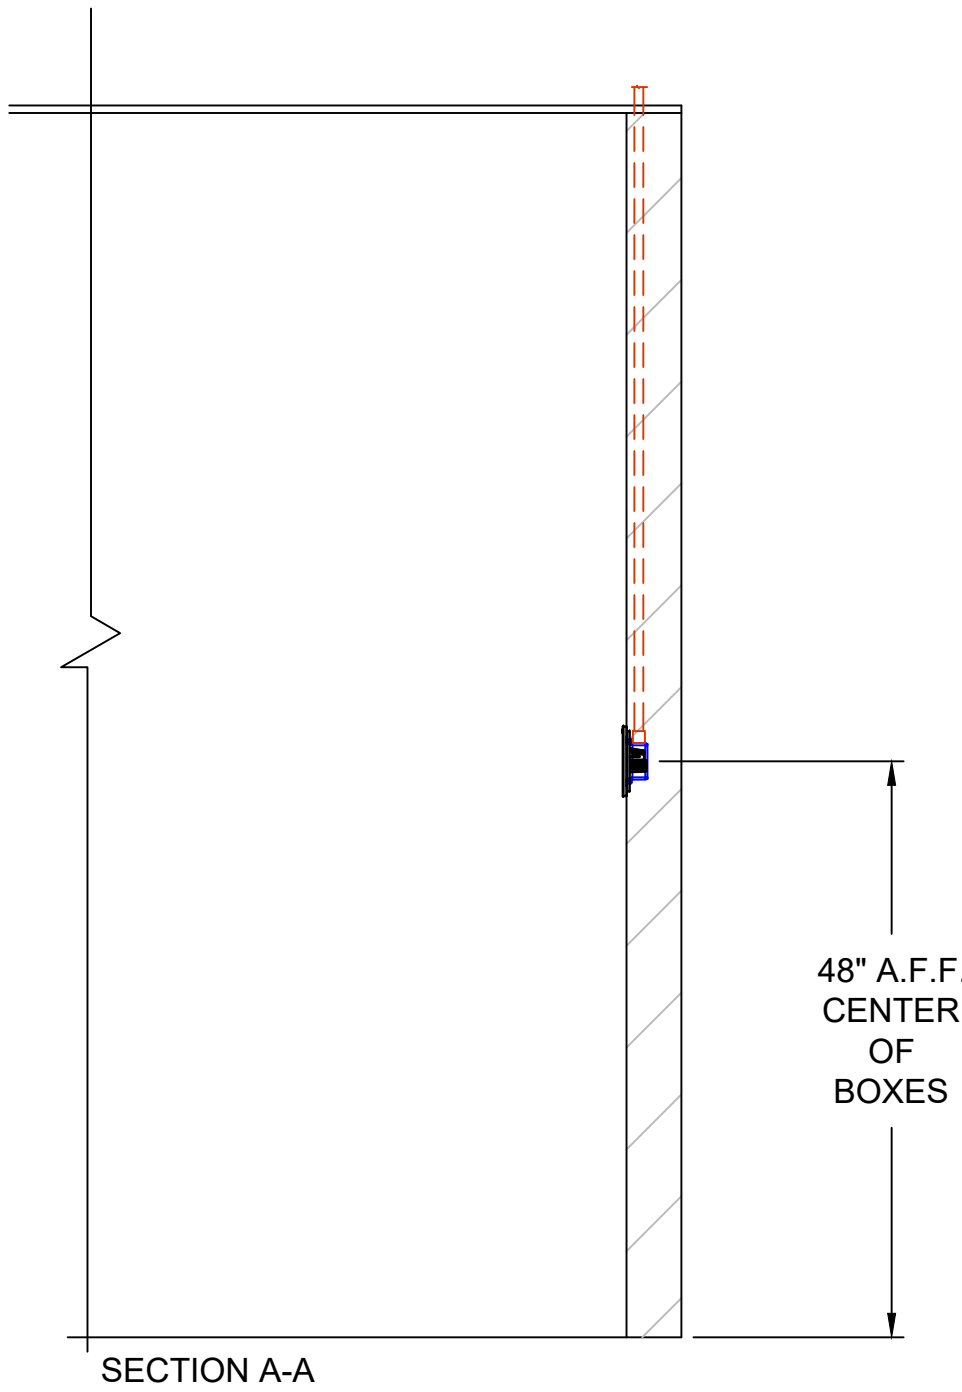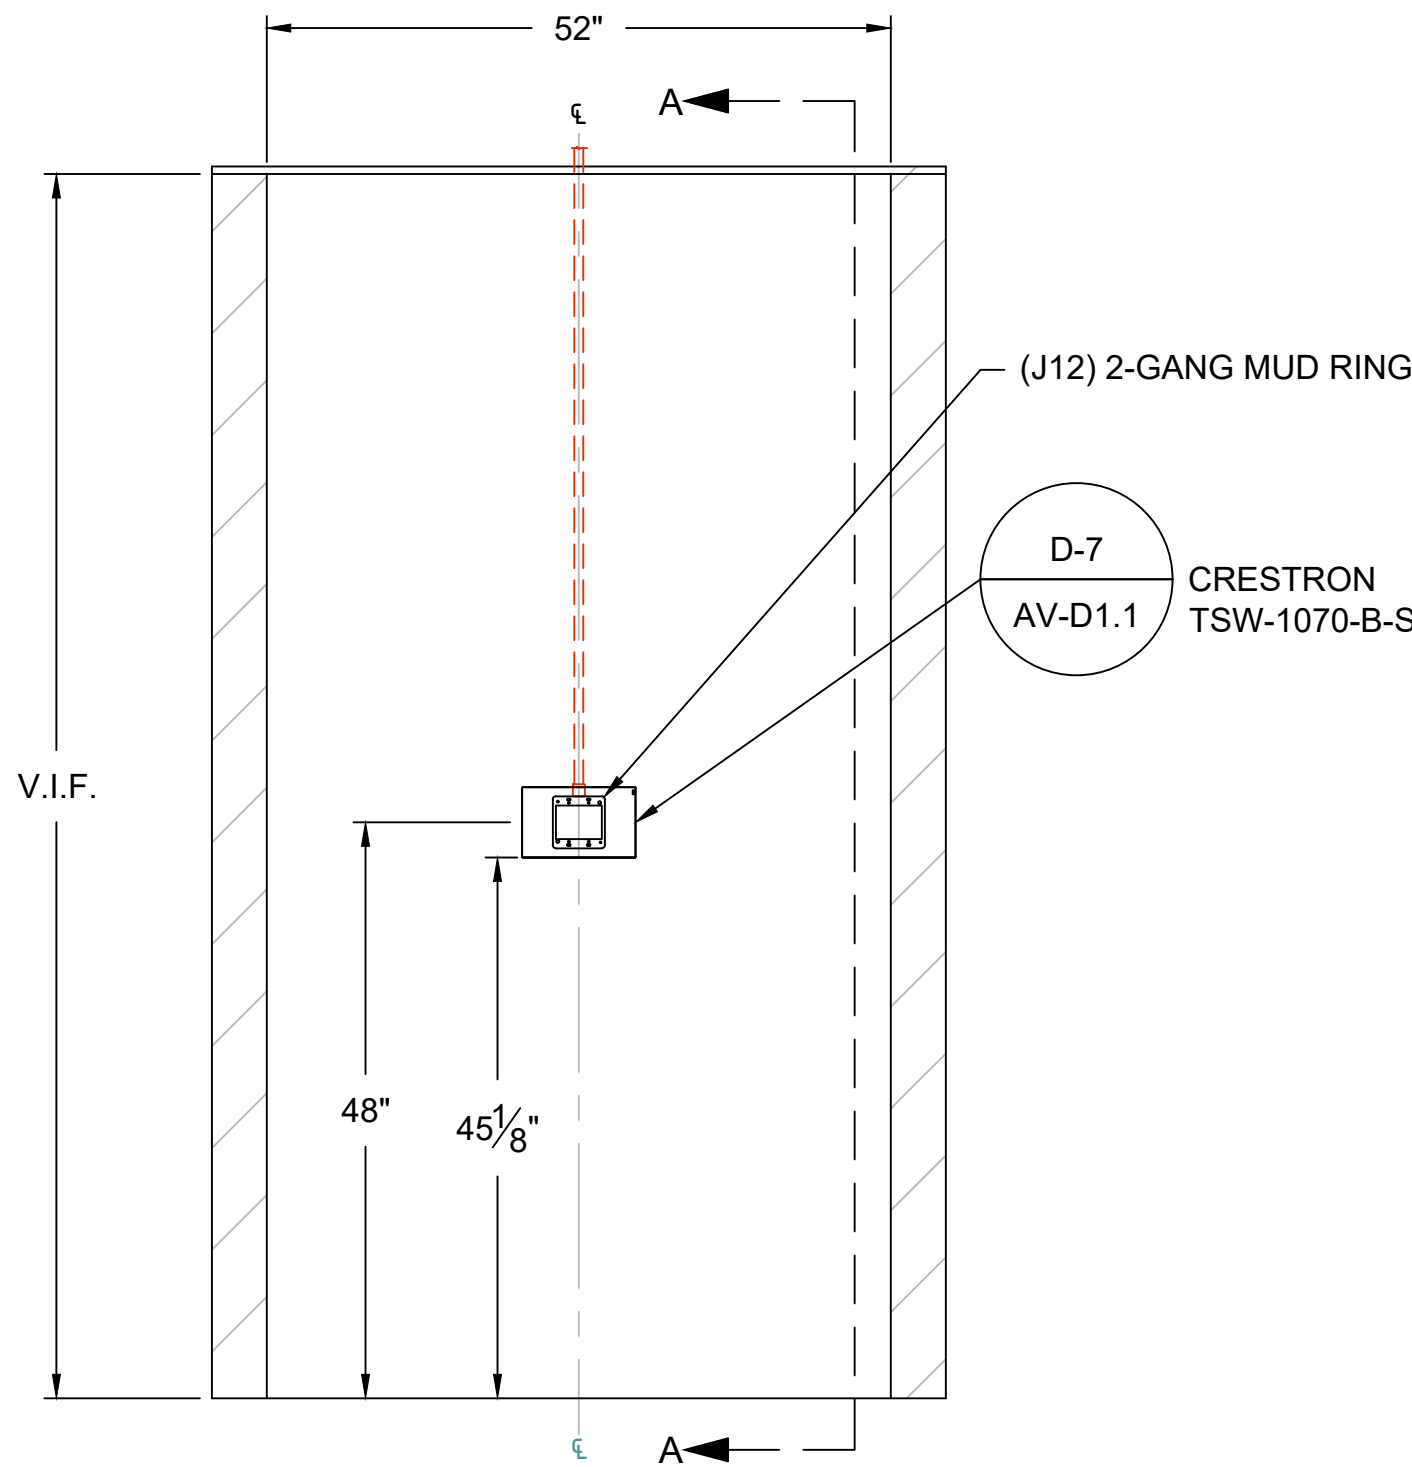

- ARCHITECTURE COLOR LEGEND:
- OWNER FURNISHED EQUIPMENT WILL BE IN BLUE
 - EXISTING EQUIPMENT WILL BE IN GREEN
 - NEW EQUIPMENT WILL BE IN BLACK

COMPANY
NEWTOWN
COMMUNITY CENTER

8 SIMPSON ST,
NEWTOWN, CT 06470

ARCHITECT
N/A

CONSULTANT
N/A

PREPARED & DESIGNED BY

VISIONPOINT
Bringing People Together to Work
152 Rockwell Rd. B6,
Newington, CT 06111
Phone: (860) 436-9673
Fax: (860) 436-9790

SEAL
NOT FOR
CONSTRUCTION

STATUS
☐ PROPOSAL
☐ SKETCH
☒ PRELIMINARY
☐ REFERENCE
☐ PROGRAMMING PHASE
☐ SCHEMATIC DESIGN PHASE
☐ DESIGN DEVELOPMENT PHASE
☐ CONSTRUCTION DOCUMENTS PHASE
☐ INTEGRATION
☐ AS BUILT

PROJECT INFORMATION
PROJECT NAME: NEWTOWN
COMMUNITY CENTER
PROJECT NUMBER: P1579
PROJECT START DATE: 08/05/2026
ENGINEERED BY: KR
DRAWN BY: AVDL
SALES: MO
PROJECT MANAGER: GA
CHECKED BY: DG & MG
SCALE: NONE

LEGAL NOTICE
COPYRIGHT 2026, VISIONPOINT LLC.
ALL DRAWINGS AND WRITTEN MATERIAL
HEREIN CONSTITUTE ORIGINAL AND
UNPUBLISHED WORK OF THE ENGINEER.
WRITTEN DIMENSIONS ON DRAWINGS
SHALL HAVE PRECEDENCE OVER SCALED
DIMENSIONS. CONTRACTORS SHALL
VERIFY AND BE RESPONSIBLE FOR
DIMENSIONS. VISIONPOINT LLC MUST BE
NOTIFIED OF ANY DEVIATIONS FROM
DIMENSIONS OR CONDITIONS OF SAID
DRAWINGS. SHOP DRAWINGS MUST BE
SUBMITTED FOR APPROVAL BEFORE
PROCEEDING.

STAMP



DATE:
BY:
This review is only for general conformance
with the design concept of the project and
general compliance with the information given
in the contract documents. Contractor is
responsible for dimension to be confirmed and
corrected at the place. Information that
pertains solely to the fabrication processes or
to the means, methods, techniques,
sequences, and procedures of construction;
coordination of the of all trades; and for
performing all work in a safe and satisfactory
manner.

REVISION NUMBER
REVISION #1: XXXXXXXX
REVISION #2: XXXXXXXX
REVISION #3: XXXXXXXX
REVISION #4: XXXXXXXX
REVISION #5: XXXXXXXX
REVISION #6: XXXXXXXX

RELEASE DATE
08/05/2026

TITLE
MULTIPURPOSE 1 ROOM 170
PLAN NORTH WALL, WALL
ELEVATION & SECTION
VIEWS


DRAWING
AV-E1.5

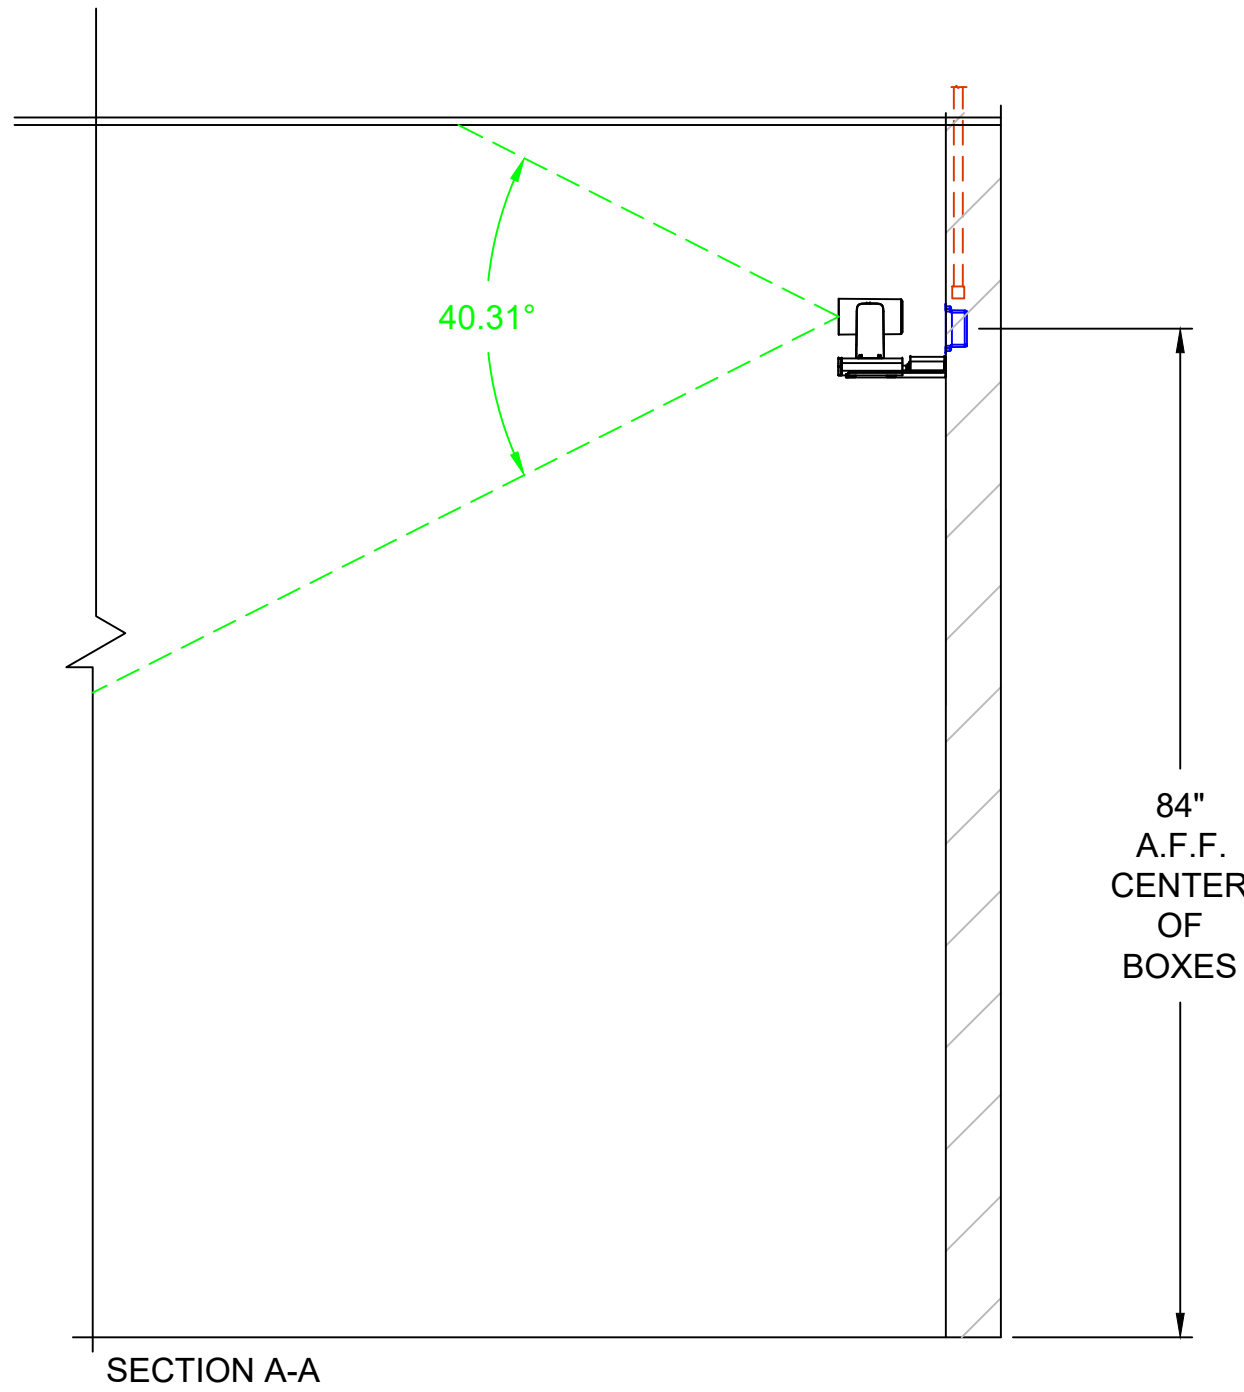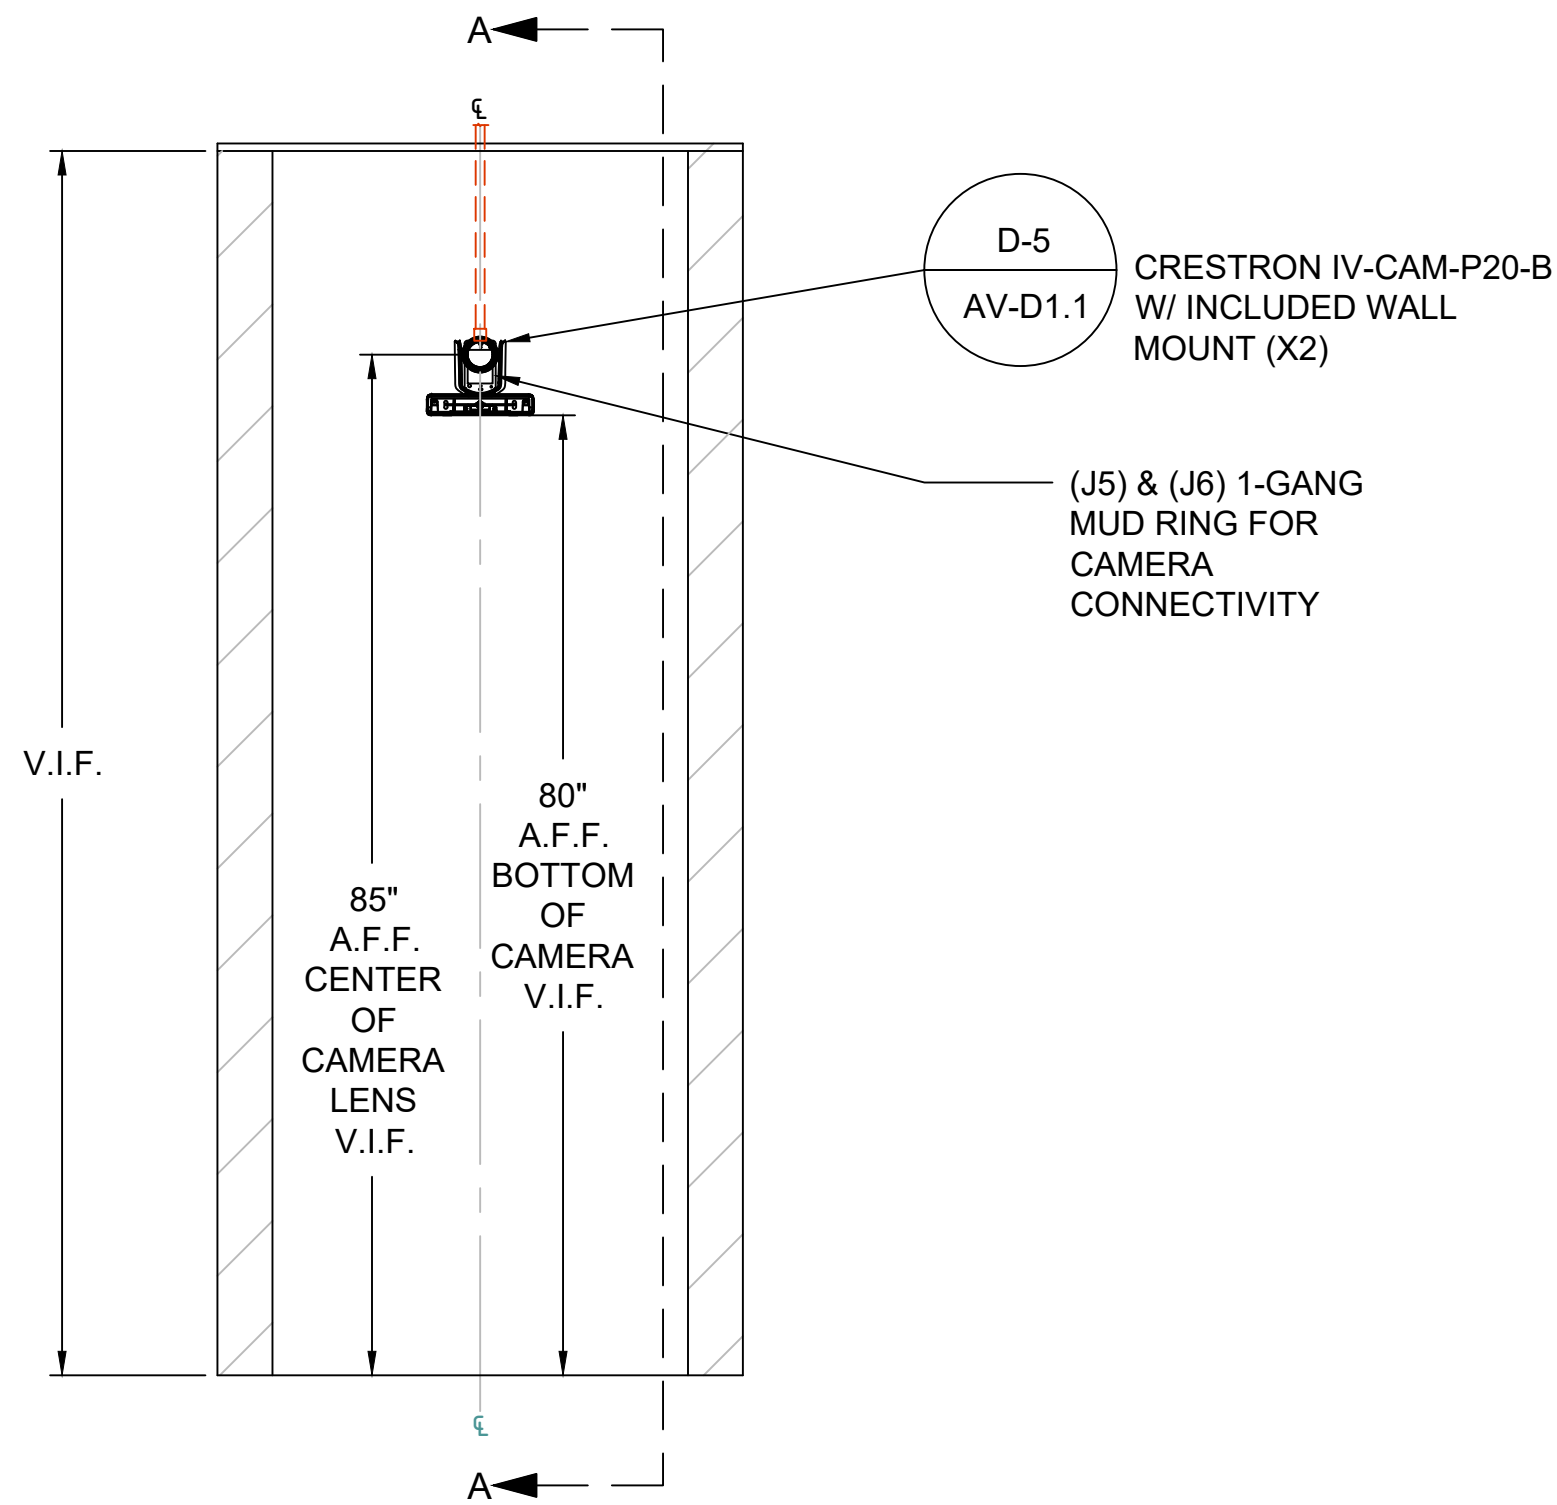


- ARCHITECTURE COLOR LEGEND:**
- OWNER FURNISHED EQUIPMENT WILL BE IN BLUE
 - EXISTING EQUIPMENT WILL BE IN GREEN
 - NEW EQUIPMENT WILL BE IN BLACK

1 WALL ELEVATION DETAIL [COMMUNITY CENTER]
SCALE: 3/4"=1'-0" ARCH D


COMPANY
NEWTOWN COMMUNITY CENTER
8 SIMPSON ST, NEWTOWN, CT 06470
ARCHITECT
N/A
CONSULTANT
N/A
PREPARED & DESIGNED BY
 VISIONPOINT Bringing People Together to Work 152 Rockwell Rd. B6, Newington, CT 06111 Phone: (860) 436-9673 Fax: (860) 436-9790
SEAL
NOT FOR CONSTRUCTION
STATUS ☐ PROPOSAL ☐ SKETCH ☒ PRELIMINARY ☐ REFERENCE ☐ PROGRAMMING PHASE ☐ SCHEMATIC DESIGN PHASE ☐ DESIGN DEVELOPMENT PHASE ☐ CONSTRUCTION DOCUMENTS PHASE ☐ INTEGRATION ☐ AS BUILT
PROJECT INFORMATION
PROJECT NAME: NEWTOWN COMMUNITY CENTER
PROJECT NUMBER: P1579
PROJECT START DATE: 08/05/2026
ENGINEERED BY: KR
DRAWN BY: AVDL
SALES: MO
PROJECT MANAGER: GA
CHECKED BY: DG & MG
SCALE: NONE
LEGAL NOTICE COPYRIGHT 2026, VISIONPOINT LLC. ALL DRAWINGS AND WRITTEN MATERIAL HEREIN CONSTITUTE ORIGINAL AND UNPUBLISHED WORK OF THE ENGINEER. WRITTEN DIMENSIONS ON DRAWINGS SHALL HAVE PRECEDENCE OVER SCALED DIMENSIONS. CONTRACTORS SHALL VERIFY AND BE RESPONSIBLE FOR DIMENSIONS. VISIONPOINT LLC MUST BE NOTIFIED OF ANY DEVIATIONS FROM DIMENSIONS OR CONDITIONS OF SAID DRAWINGS. SHOP DRAWINGS MUST BE SUBMITTED FOR APPROVAL BEFORE PROCEEDING.
STAMP
DATE: BY: This review is only for general conformance with the design concept of the project and general compliance with the information given in the contract documents. Contractor is responsible for dimension to be confirmed and corrected at the place. Information that pertains solely to the fabrication processes or to the means, methods, techniques, equipment, and procedures of construction; coordination of the of all trades; and for performing all work in a safe and satisfactory manner.
REVISION NUMBER
REVISION #1: XXXXXXXXXX
REVISION #2: XXXXXXXXXX
REVISION #3: XXXXXXXXXX
REVISION #4: XXXXXXXXXX
REVISION #5: XXXXXXXXXX
REVISION #6: XXXXXXXXXX
RELEASE DATE
08/05/2026
TITLE
MULTIPURPOSE 3 ROOM 170 PLAN NORTH WALL, WALL ELEVATION & SECTION VIEWS
DRAWING
AV-E1.6

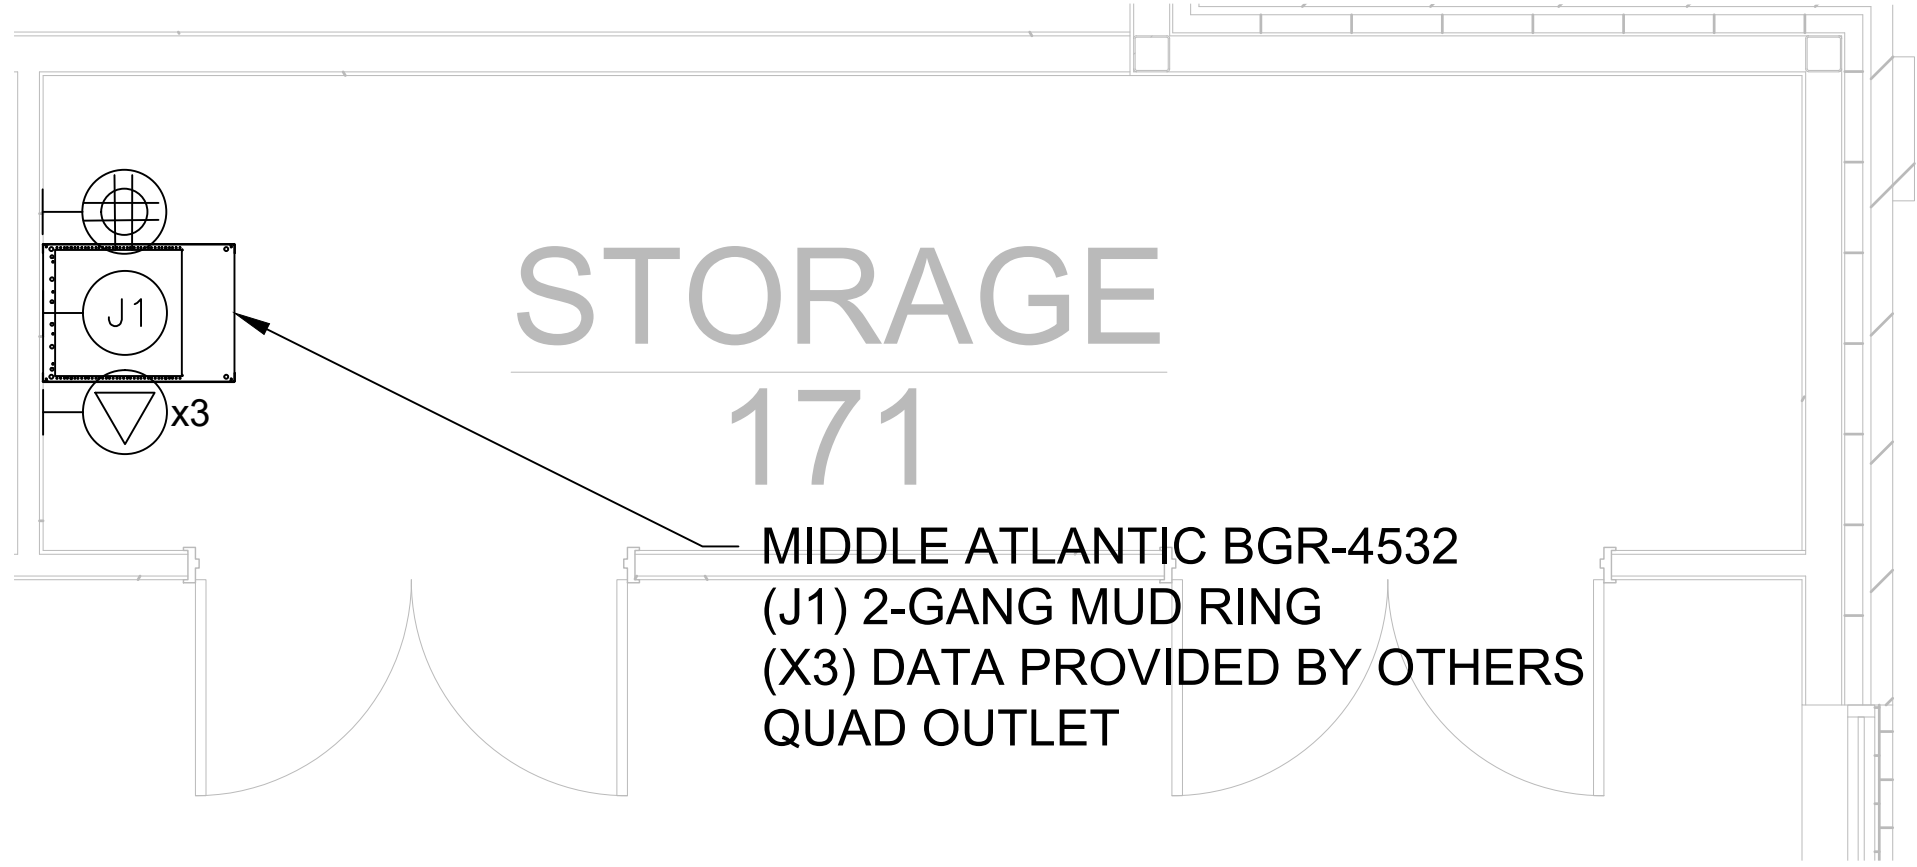

1 AV RACK CLOSET (STORAGE 171)
SCALE: 3/8"=1'-0" ARCH D

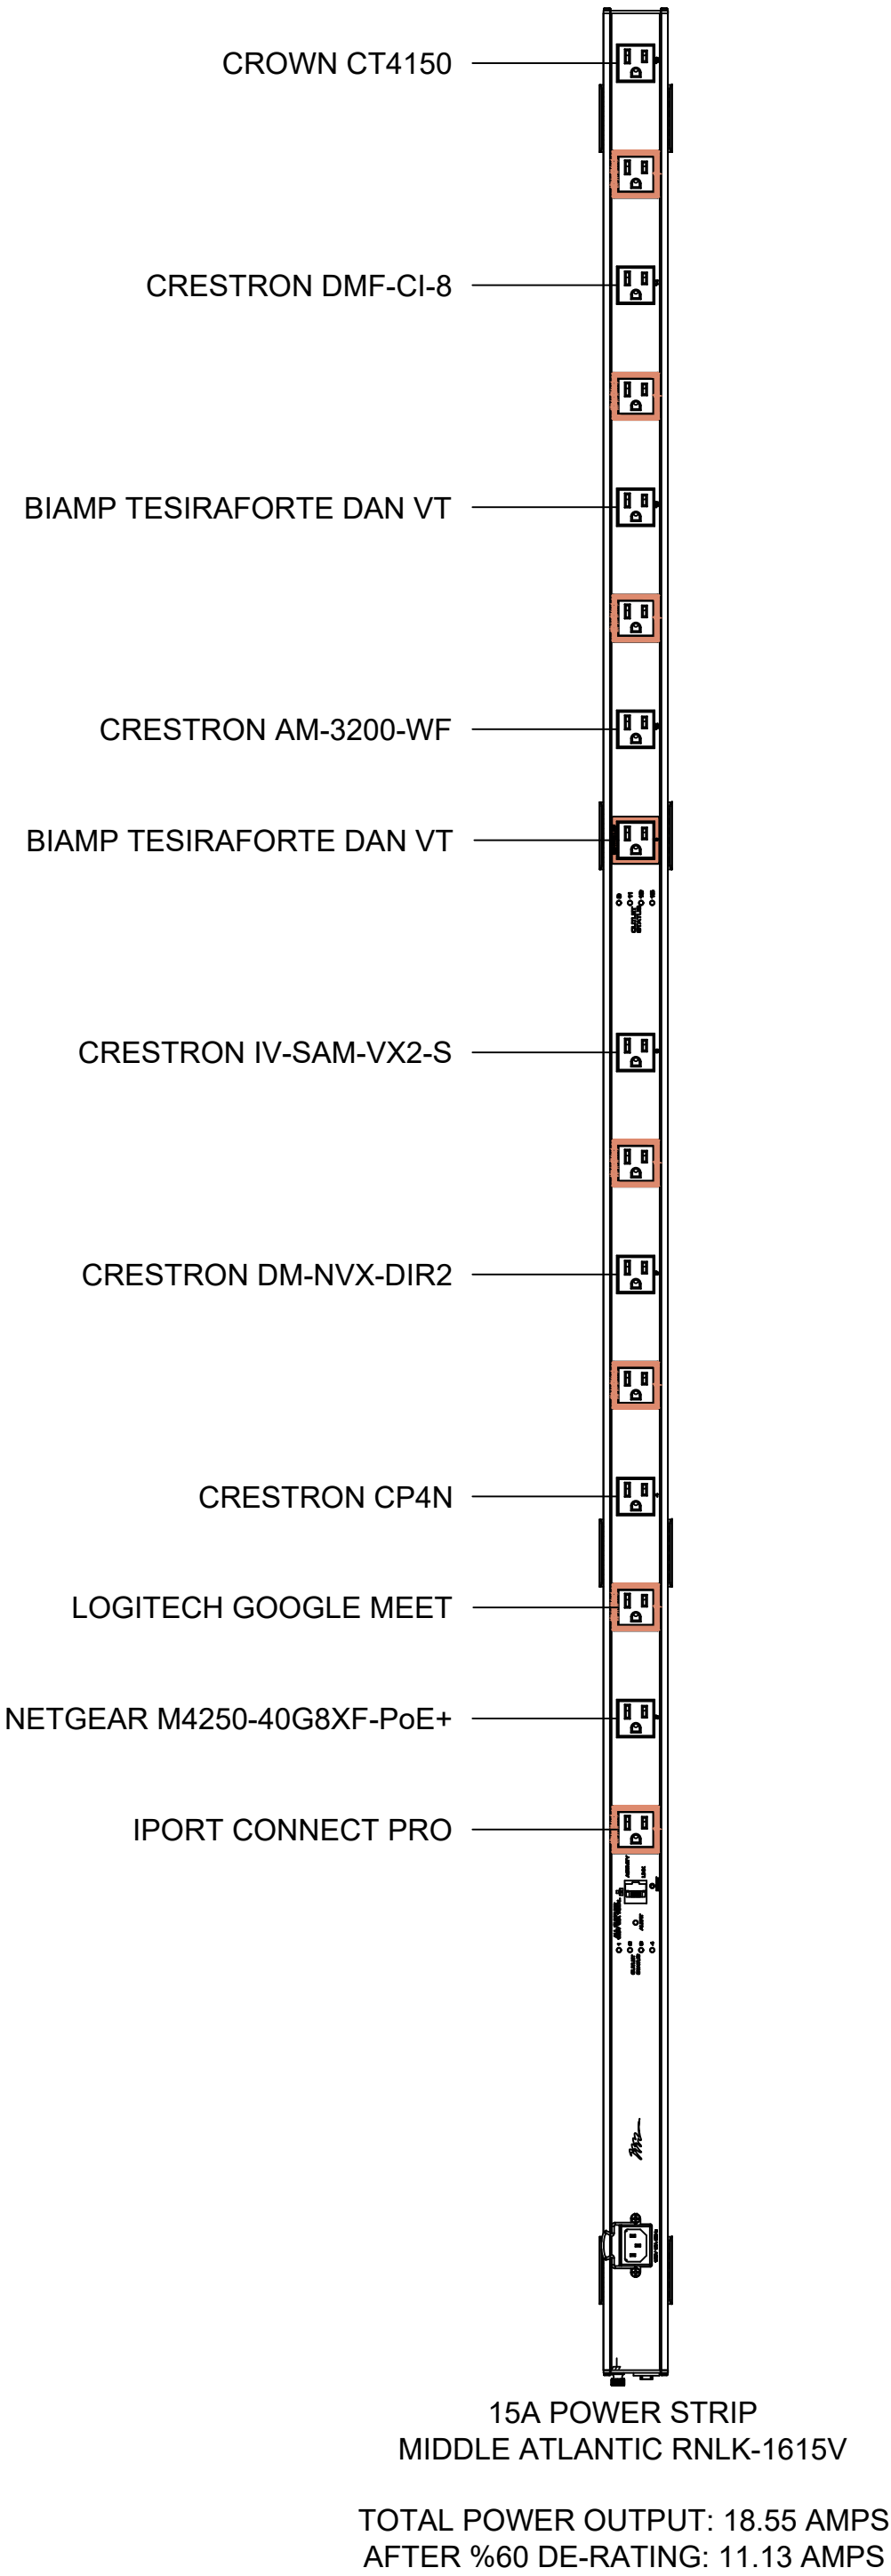

RACK POWER CALCULATIONS							%60 DE-RATED AMPS	%60 DE-RATED BTU
MANUFACTURER	MODEL	QTY.	VOLTS	WATTS	AMPS	BTU		
NETGEAR	M4250-40G8XF-PoE+	1	120	1197	9.98	4086.56		
CRESTRON	CP4N	1	120	15	0.13	50		
CRESTRON	DM-NVX-DIR2	1	120	12.6	0.11	42.9		
CRESTRON	IV-SAM-VX2-S	1	120	400	3.33	1706		
LOGITECH	MEET COMPUTE	1	120	90	0.75	307		
CRESTRON	AM-3200-WF	1	120	14	0.12	47.8		
BIMAP	TESIRAFORTE DAN VT	2	120	70	0.58	238.8		
CRESTRON	DMF-CI-8	1	120	350	2.92	1195		
BLAZE AUDIO	POWERZONE CONNECT 254	1	120	75	0.63	256		
TOTALS			120	2223.60000 0	18.550000	7930.06000 0	11.1300	4758.036000

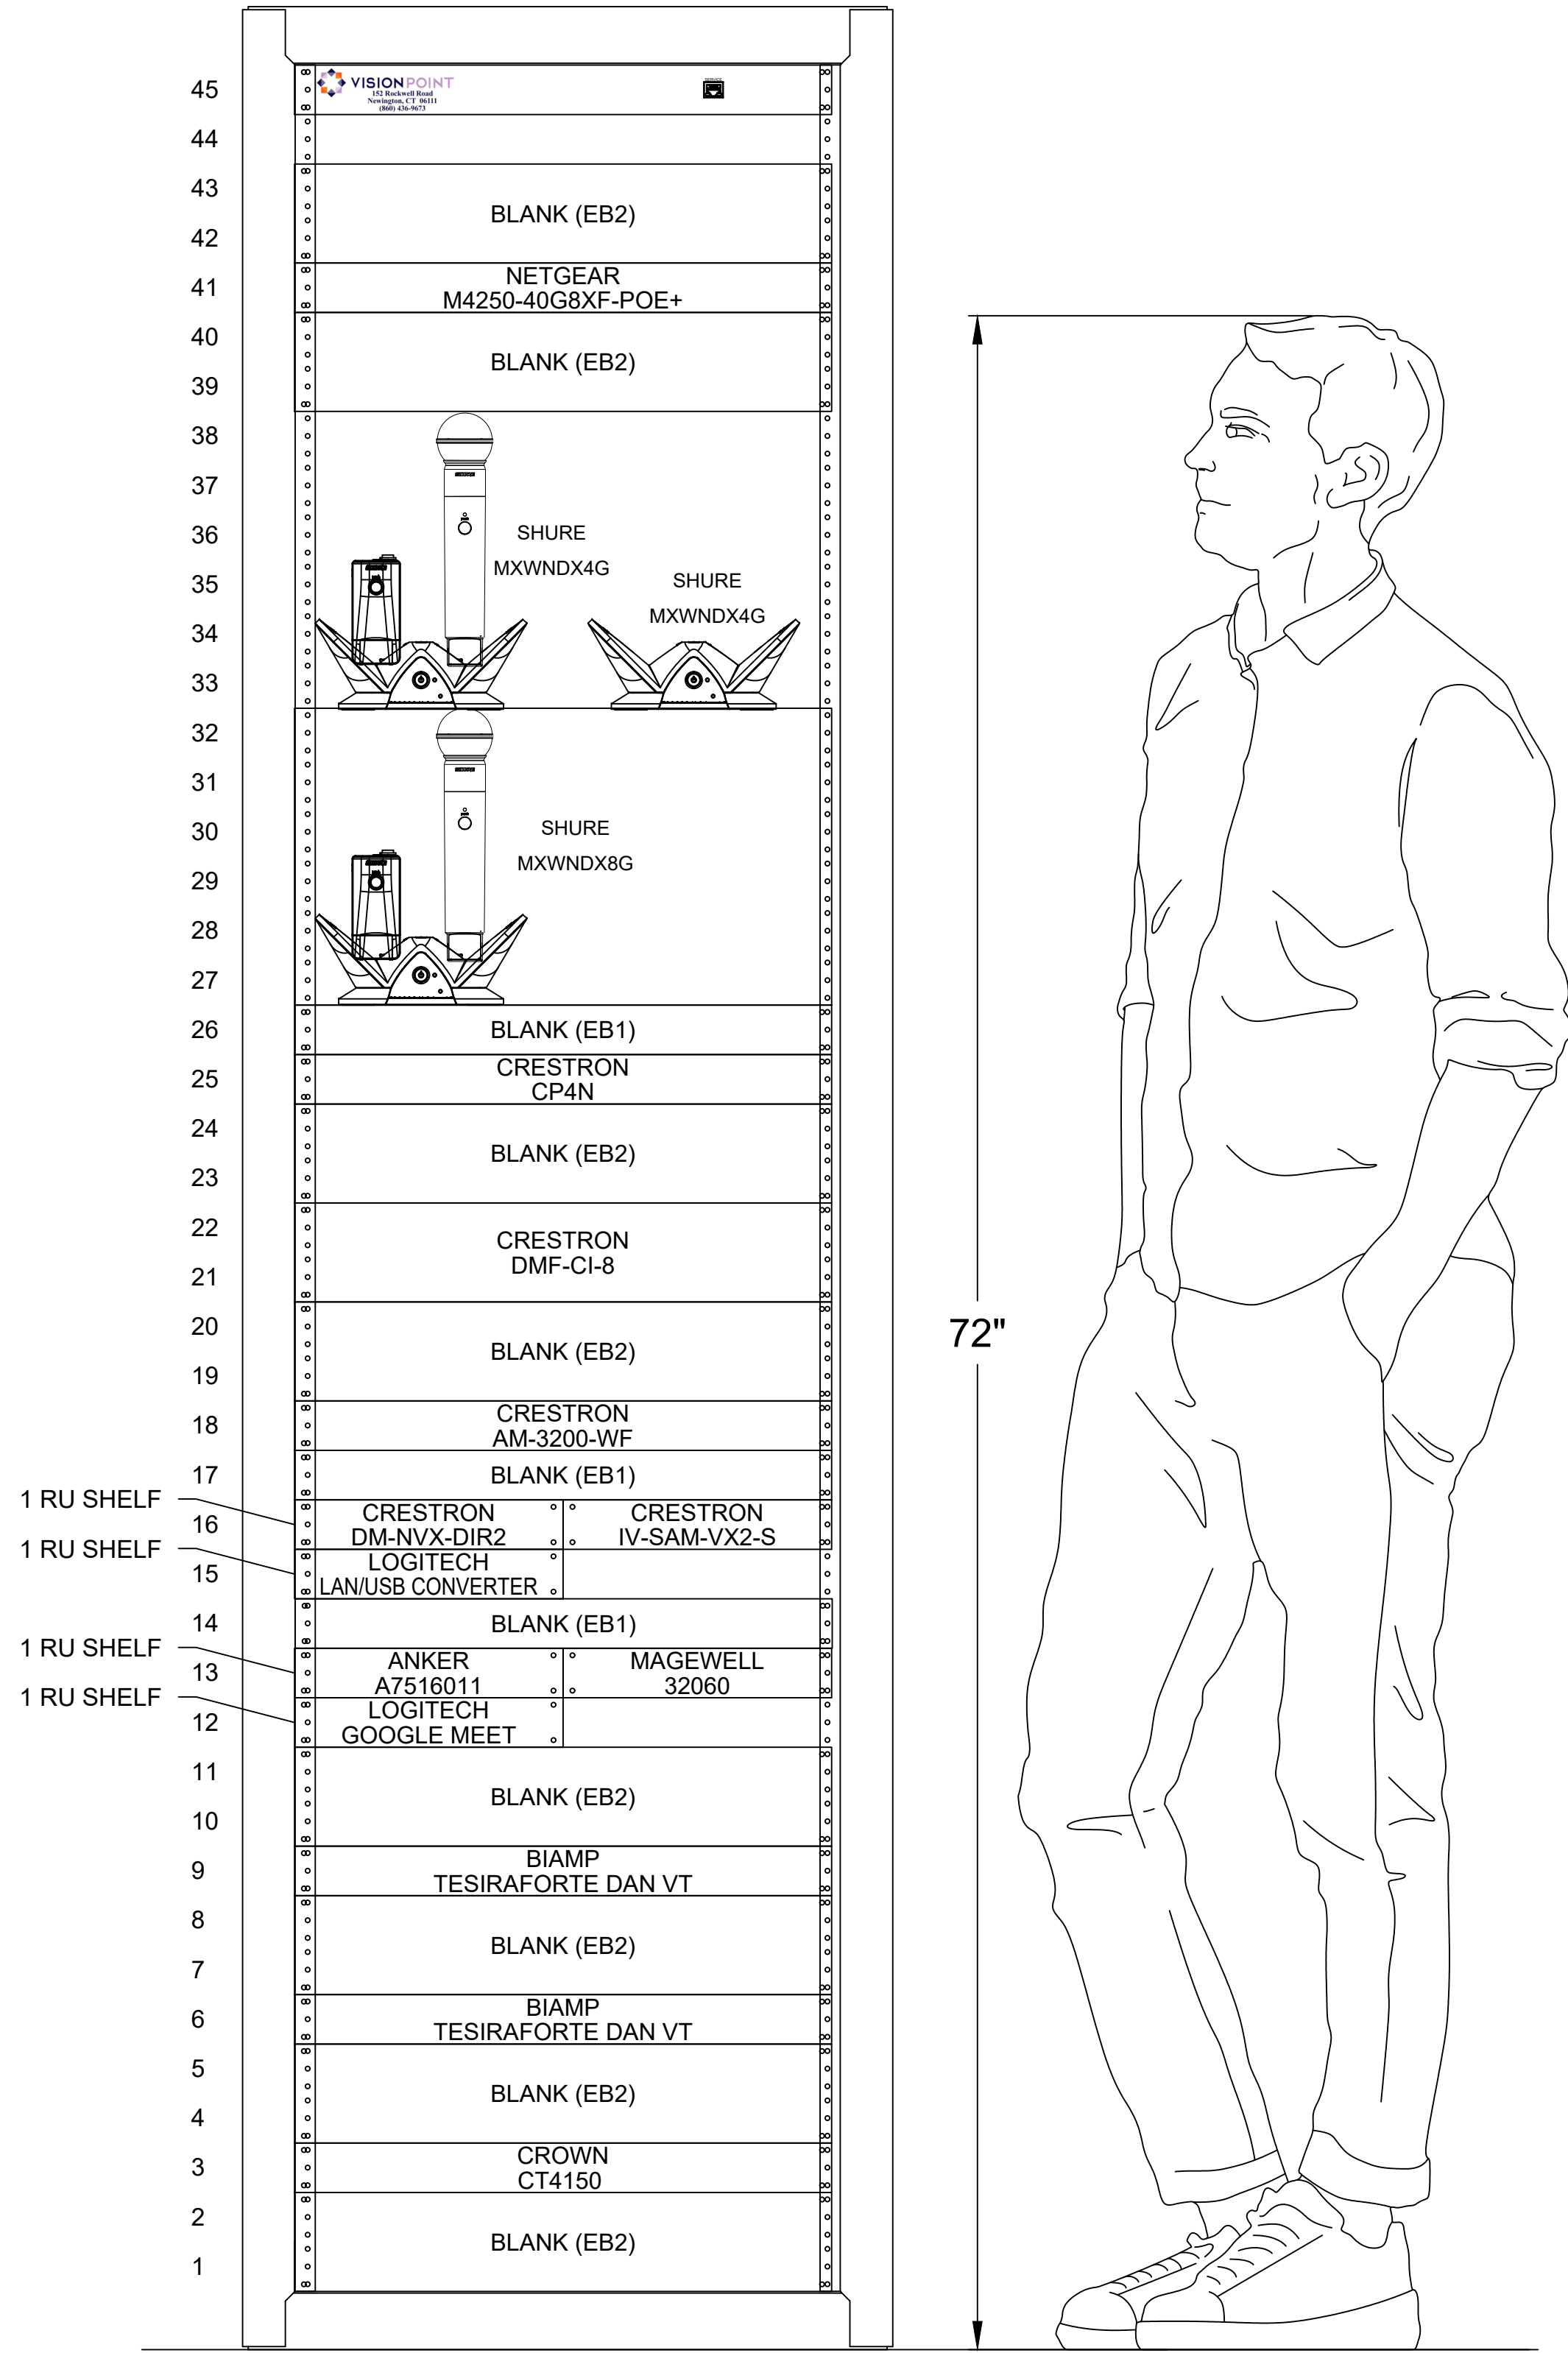

RACK SPECIFICATIONS					
MODEL	RACK O.D. WIDTH	RACKING HEIGHT	OVERALL HEIGHT	OVERALL DEPTH	# OF RU
BGR-4532	23	78.88	82.88	32	45
CASTERS ADD 0.85" TO OVERALL HEIGHT.					

- ARCHITECTURE COLOR LEGEND:
- OWNER FURNISHED EQUIPMENT WILL BE IN BLUE
 - EXISTING EQUIPMENT WILL BE IN GREEN
 - NEW EQUIPMENT WILL BE IN BLACK

COMPANY

NEWTOWN
COMMUNITY CENTER

8 SIMPSON ST,
NEWTOWN, CT 06470

ARCHITECT

N/A

CONSULTANT

N/A

PREPARED & DESIGNED BY

VISIONPOINT

Bringing People Together to Work

152 Rockwell Rd. B6,
Newington, CT 06111
Phone: (860) 436-9673
Fax: (860) 436-9790

SEAL

NOT FOR
CONSTRUCTION

STATUS

☐ PROPOSAL
☐ SKETCH
☒ PRELIMINARY
☐ REFERENCE
☐ PROGRAMMING PHASE
☐ SCHEMATIC DESIGN PHASE
☐ DESIGN DEVELOPMENT PHASE
☐ CONSTRUCTION DOCUMENTS PHASE
☐ INTEGRATION
☐ AS BUILT

PROJECT INFORMATION

PROJECT NAME: NEWTOWN
COMMUNITY CENTER

PROJECT NUMBER: P1579

PROJECT START DATE: 08/05/2026

ENGINEERED BY: KR

DRAWN BY: AVDL

SALES: MO

PROJECT MANAGER: GA

CHECKED BY: DD & MG

SCALE: NONE

LEGAL NOTICE

COPYRIGHT 2026, VISIONPOINT LLC.
ALL DRAWINGS AND WRITTEN MATERIAL
HEREIN CONSTITUTE ORIGINAL AND
UNPUBLISHED WORK OF THE ENGINEER.
WRITTEN DIMENSIONS ON DRAWINGS
SHALL HAVE PRECEDENCE OVER SCALED
DIMENSIONS. CONTRACTORS SHALL
VERIFY AND BE RESPONSIBLE FOR
DIMENSIONS. VISIONPOINT LLC MUST BE
NOTIFIED OF ANY DEVIATIONS FROM
DIMENSIONS OR CONDITIONS OF SAID
DRAWINGS. SHOP DRAWINGS MUST BE
SUBMITTED FOR APPROVAL BEFORE
PROCEEDING.

STAMP

DATL

BY:

This review is only for general conformance
with the design concept of the project and
general compliance with the information given
in the contract documents. Contractor is
responsible for dimension to be confirmed and
corrected at the jobsite. Information that
pertains solely to the fabrication processes or
to the means, methods, techniques,
sequences, and procedures of construction;
coordination of the of all trades; and for
performing all work in a safe and satisfactory
manner.

REVISION NUMBER

REVISION #1: XXXXXXXX

REVISION #2: XXXXXXXX

REVISION #3: XXXXXXXX

REVISION #4: XXXXXXXX

REVISION #5: XXXXXXXX

REVISION #6: XXXXXXXX

RELEASE DATE


08/05/2026


TITLE

RACK ELEVATION


DRAWING

AV-R1.1

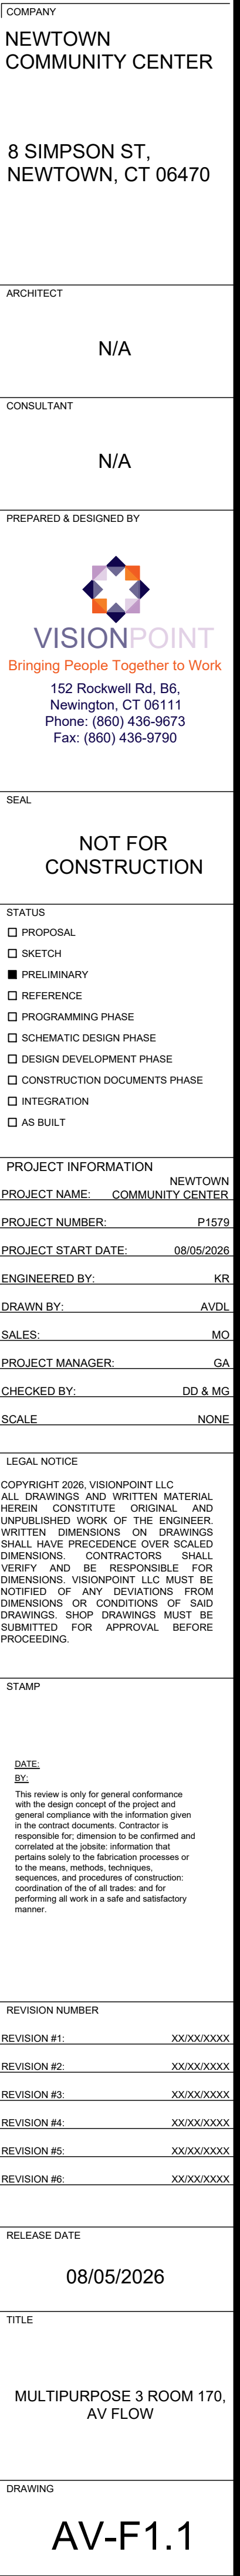


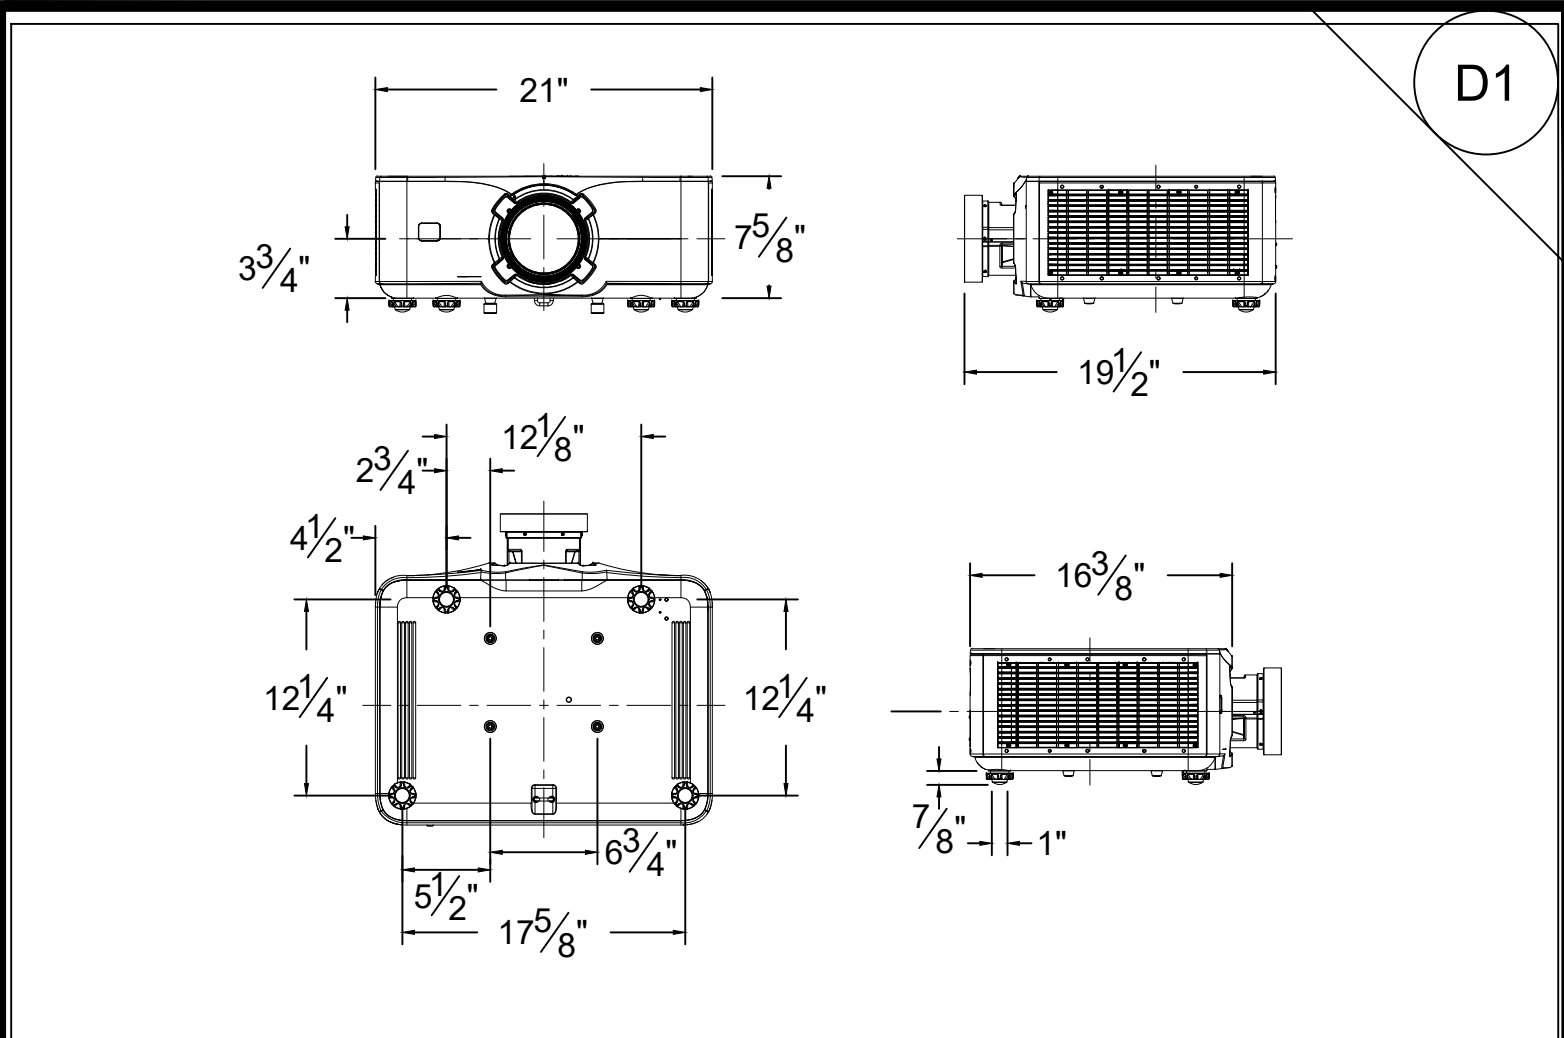


CHRISTIE 4K1000-KS

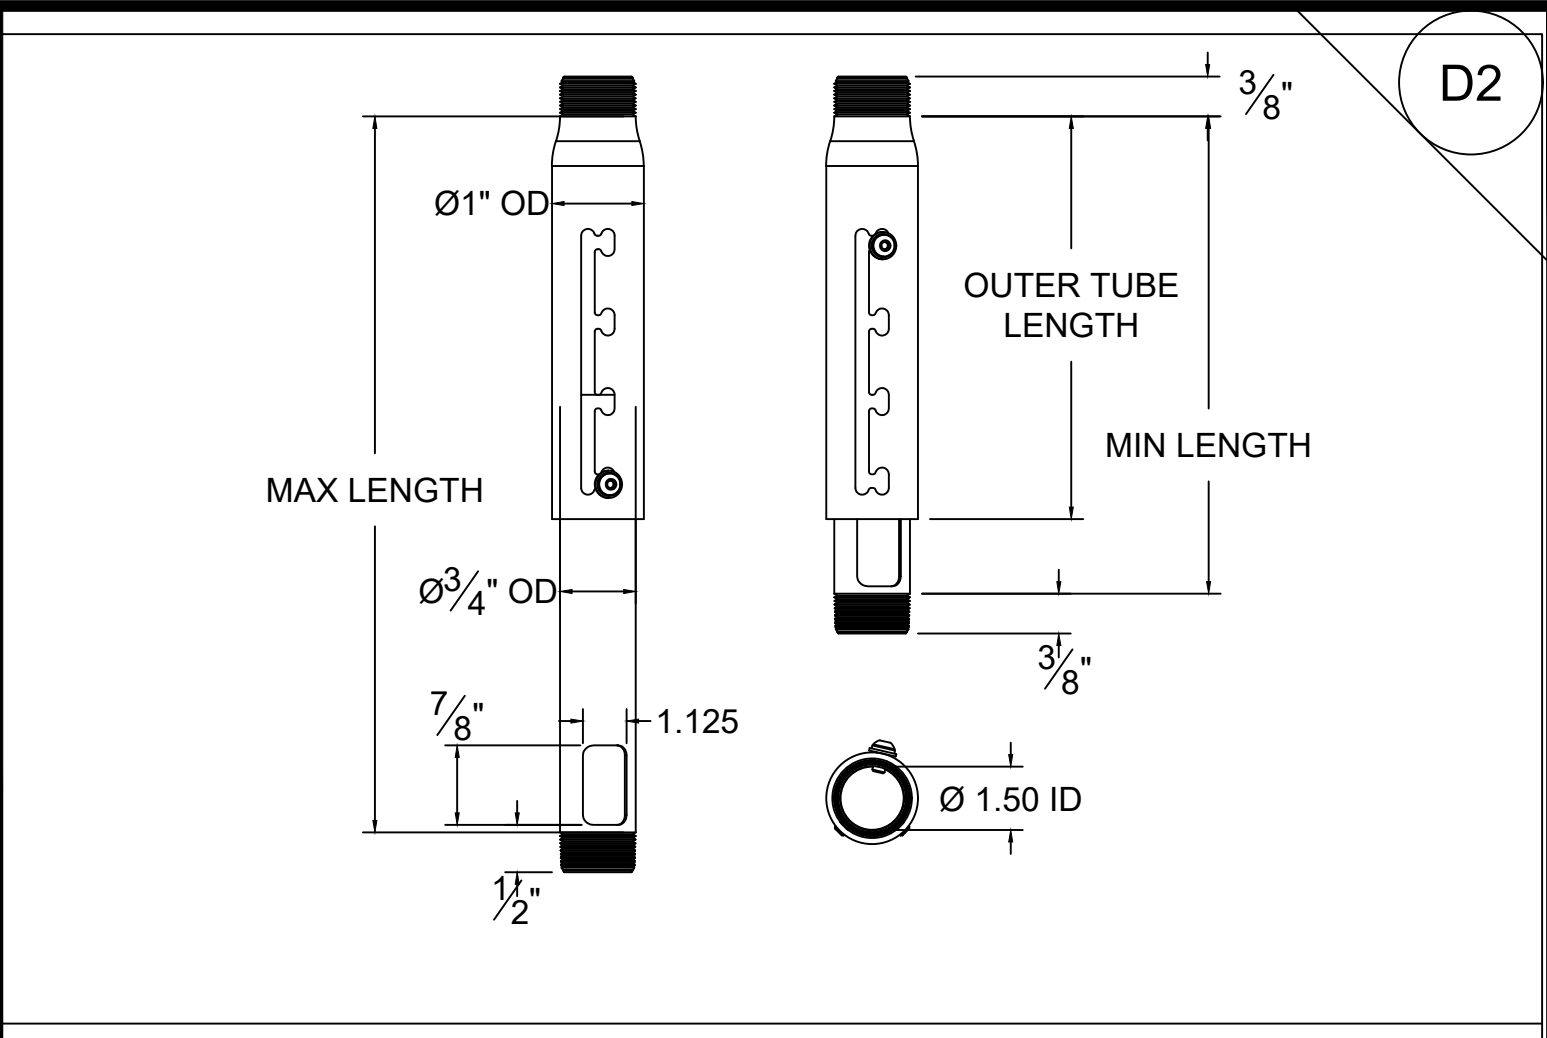


CHIEF CMS0305W

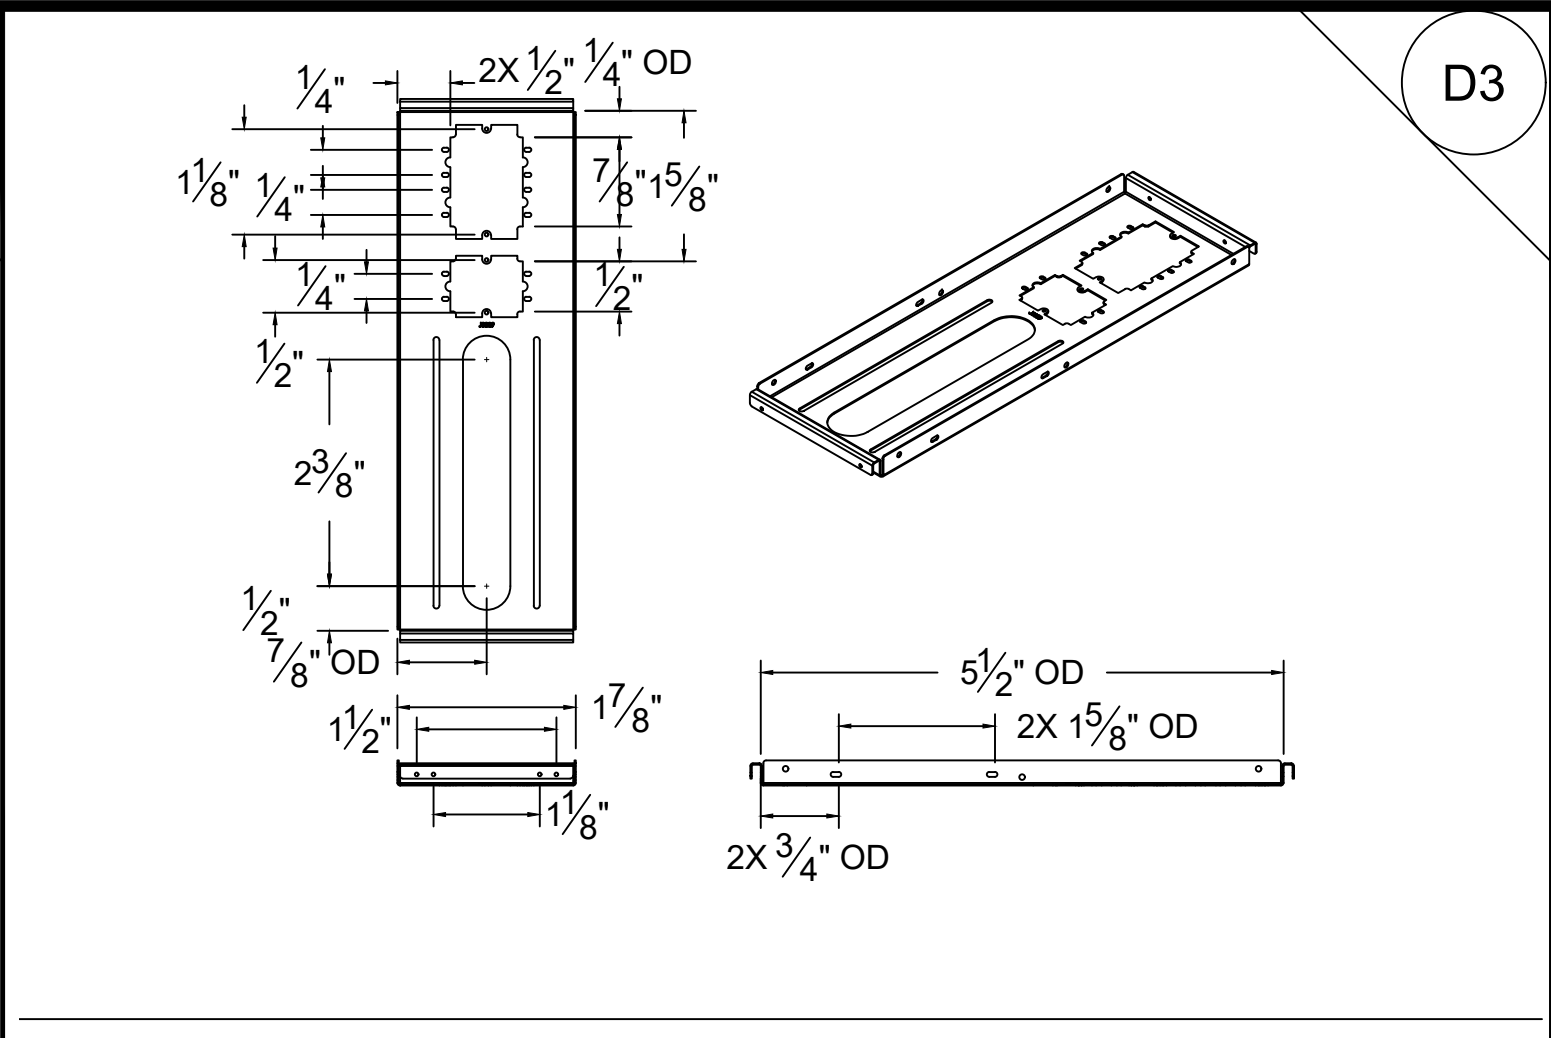


CHIEF CMS440

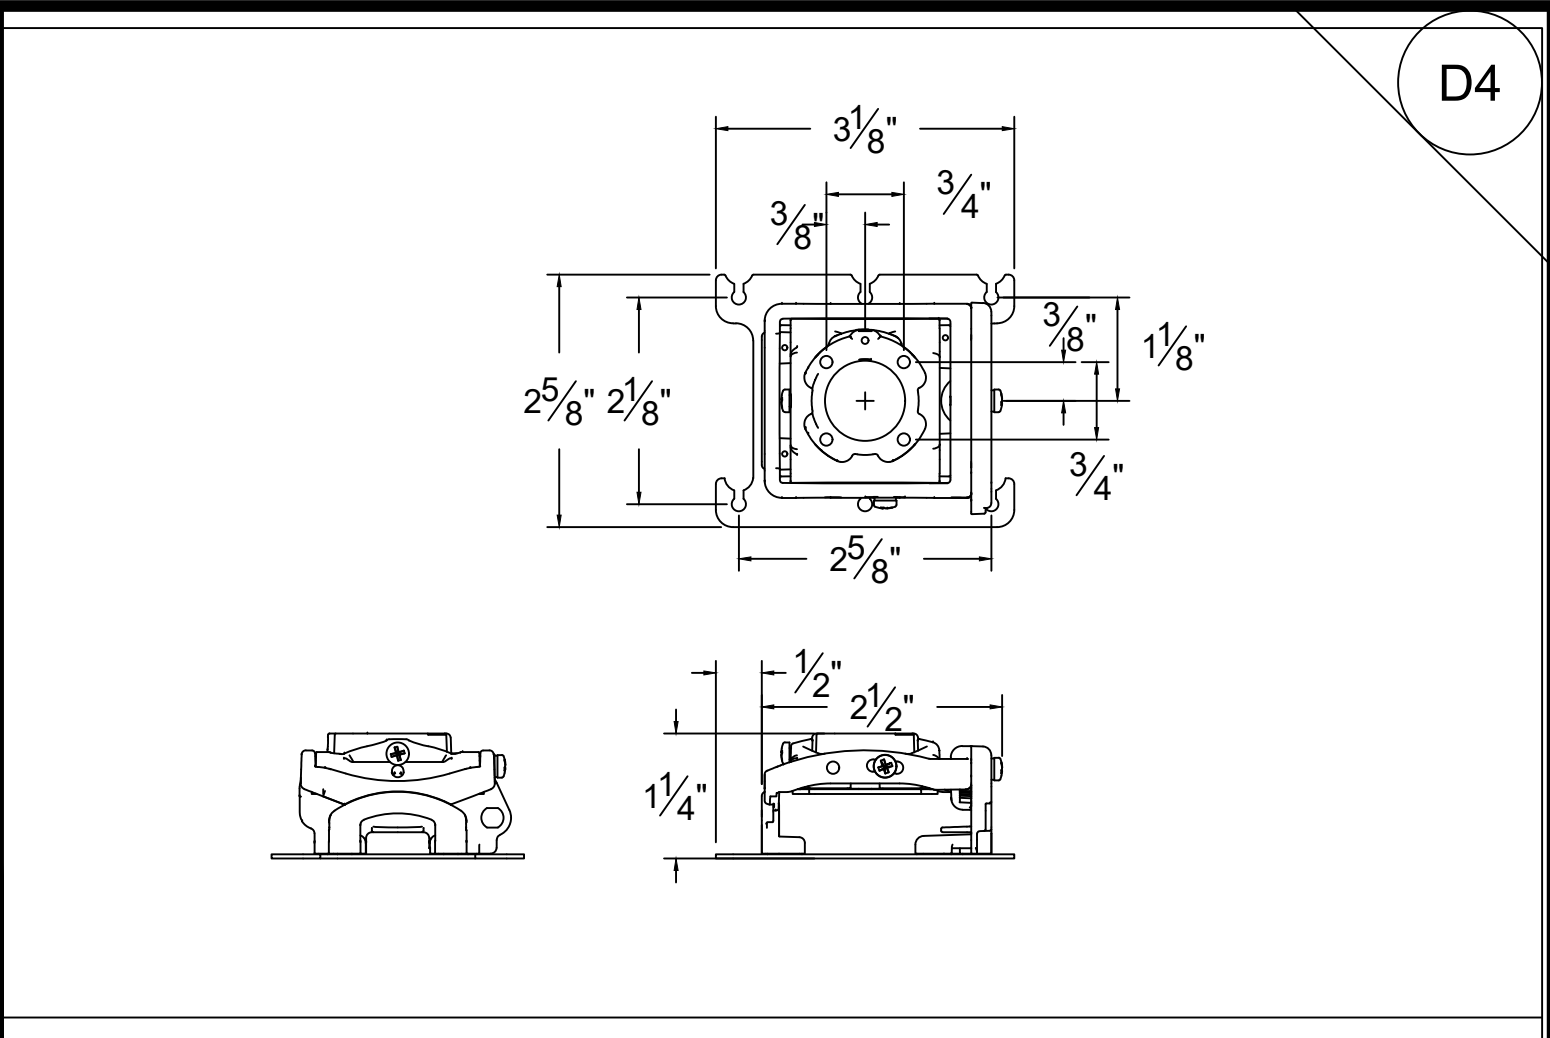


CHIEF RPMAUW

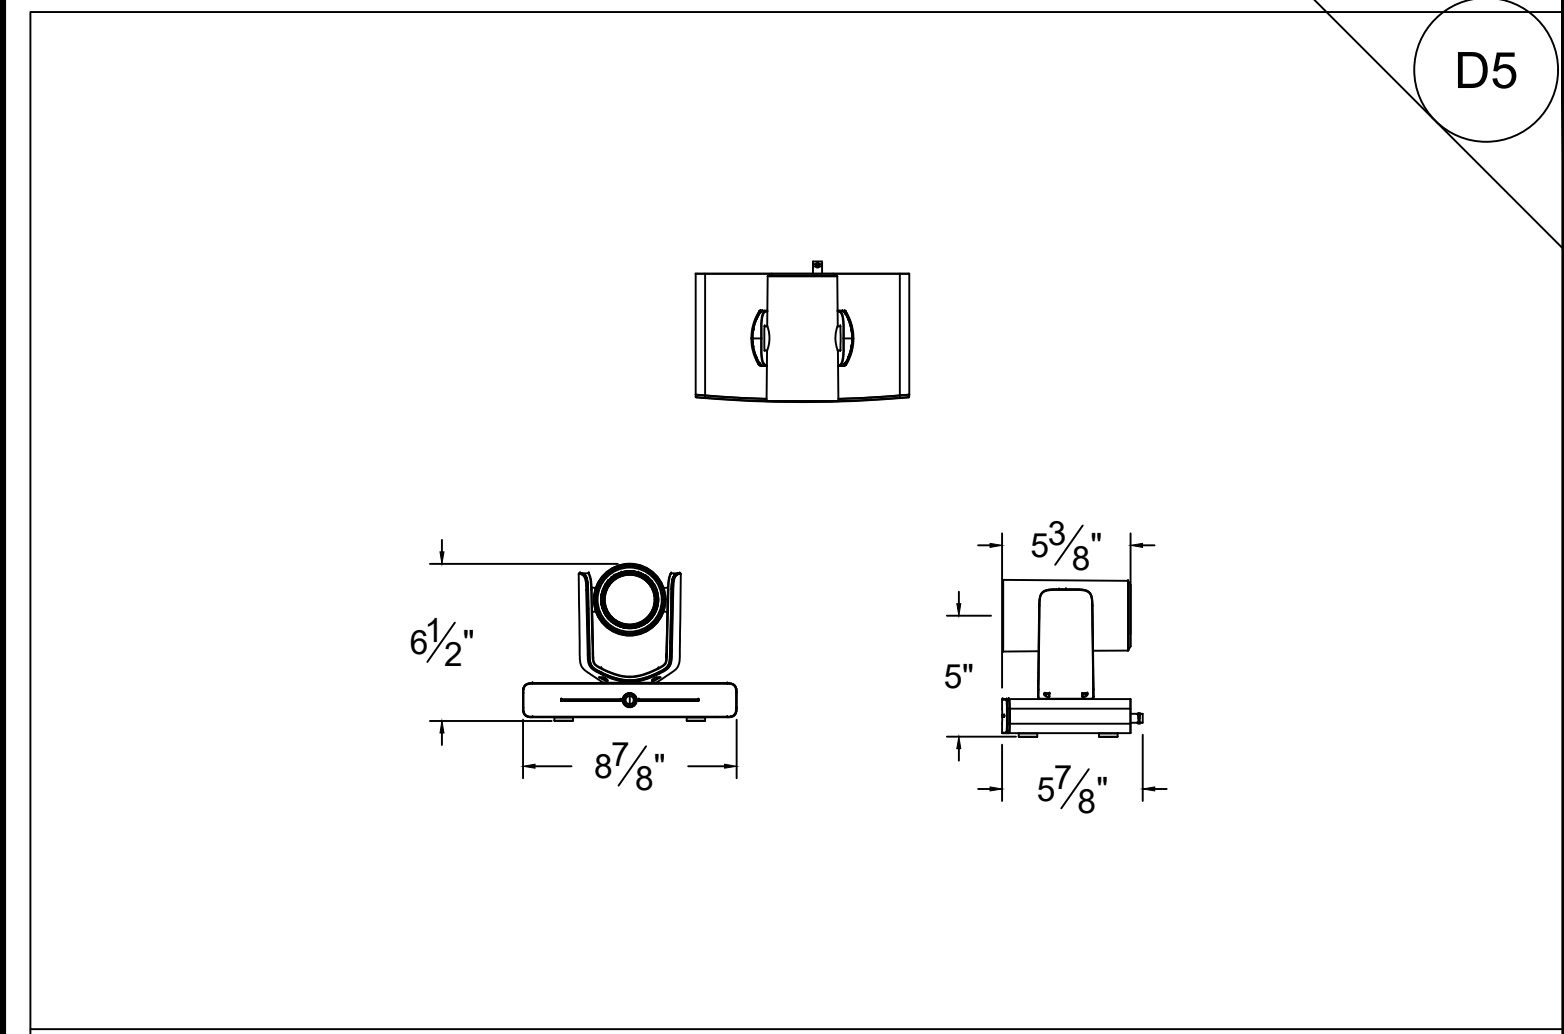


CRESTRON IV-CAM-P20

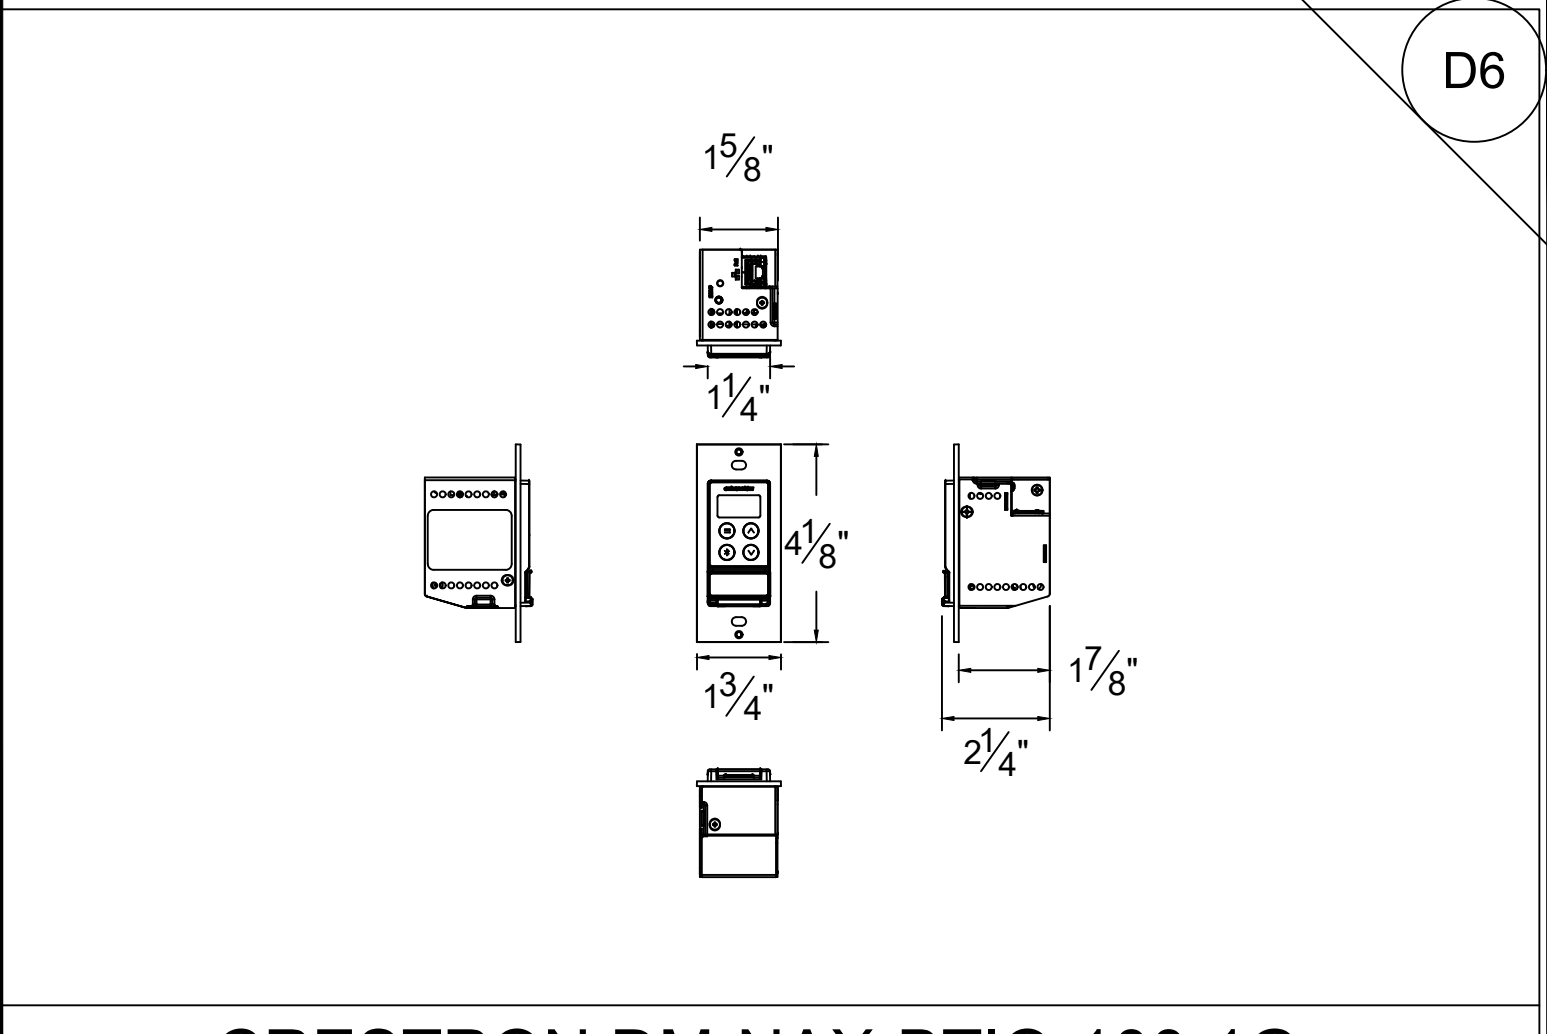


CRESTRON DM-NAX-BTIO-100-1G

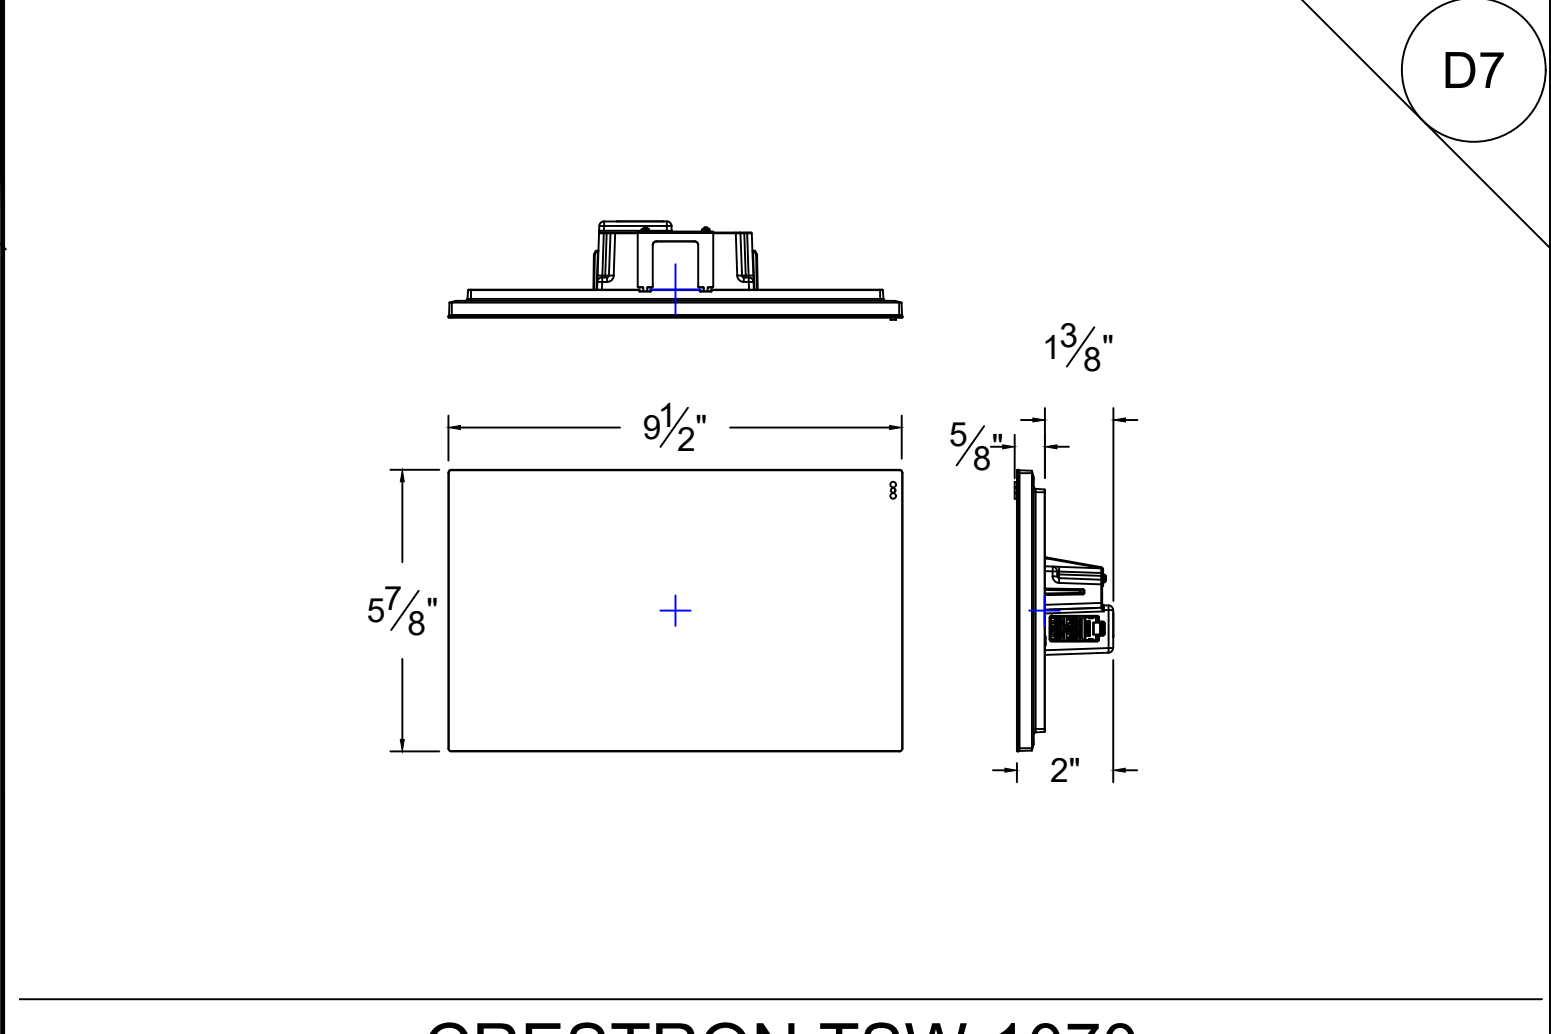

CRESTRON TSW-1070

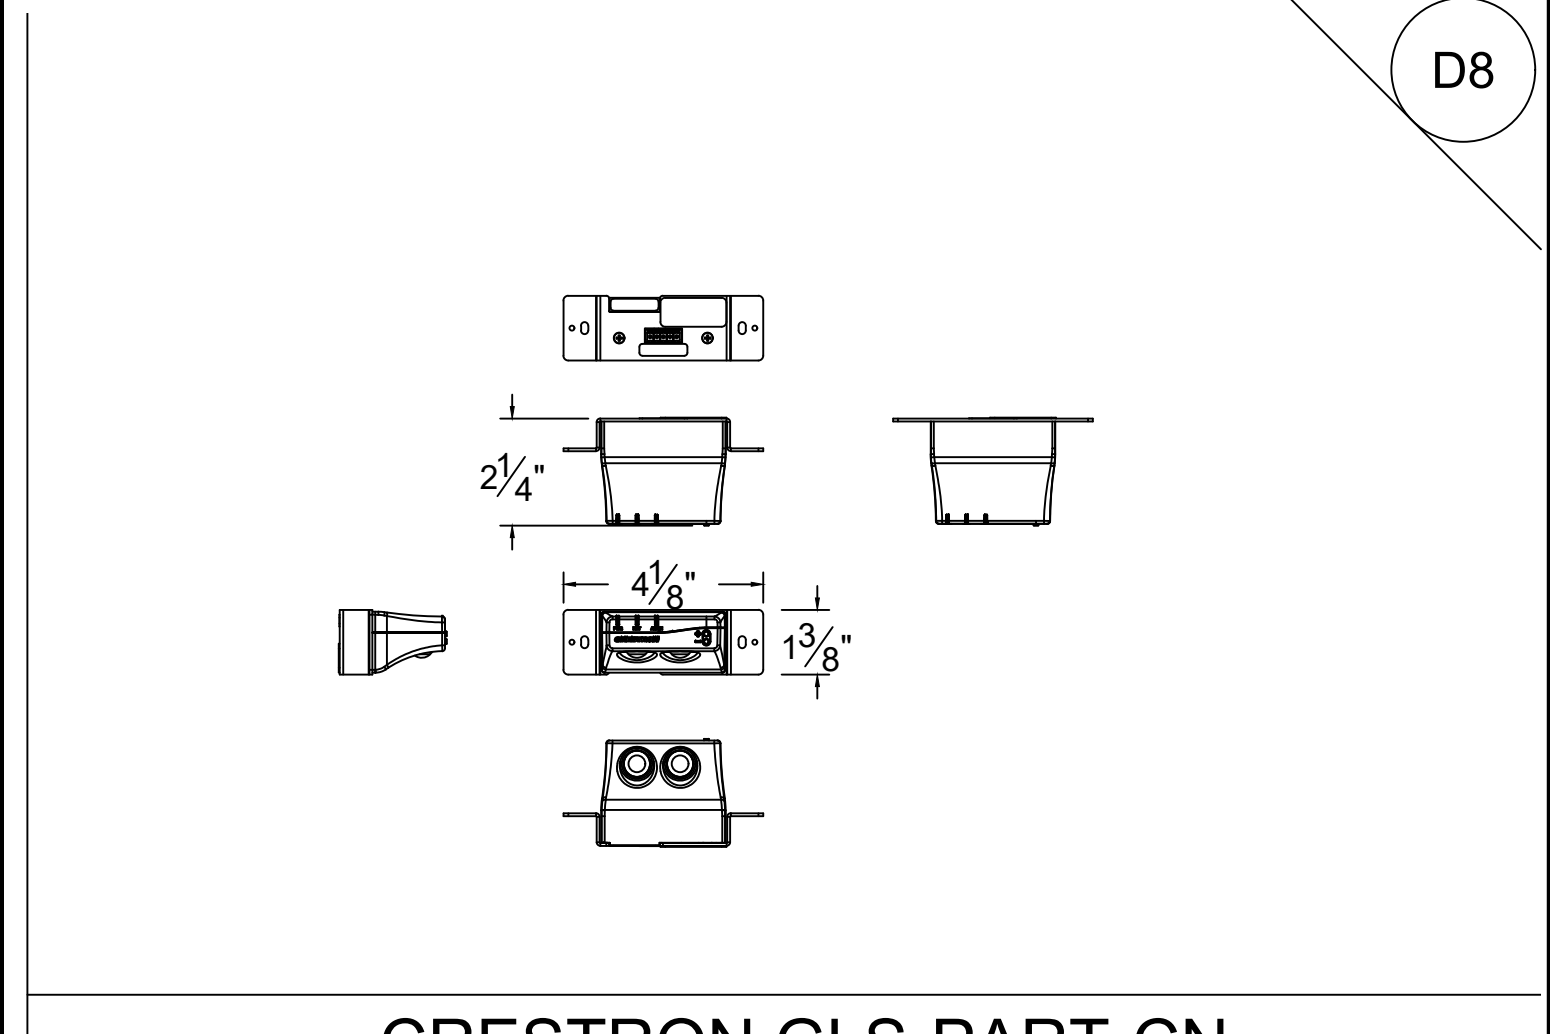

CRESTRON GLS-PART-CN

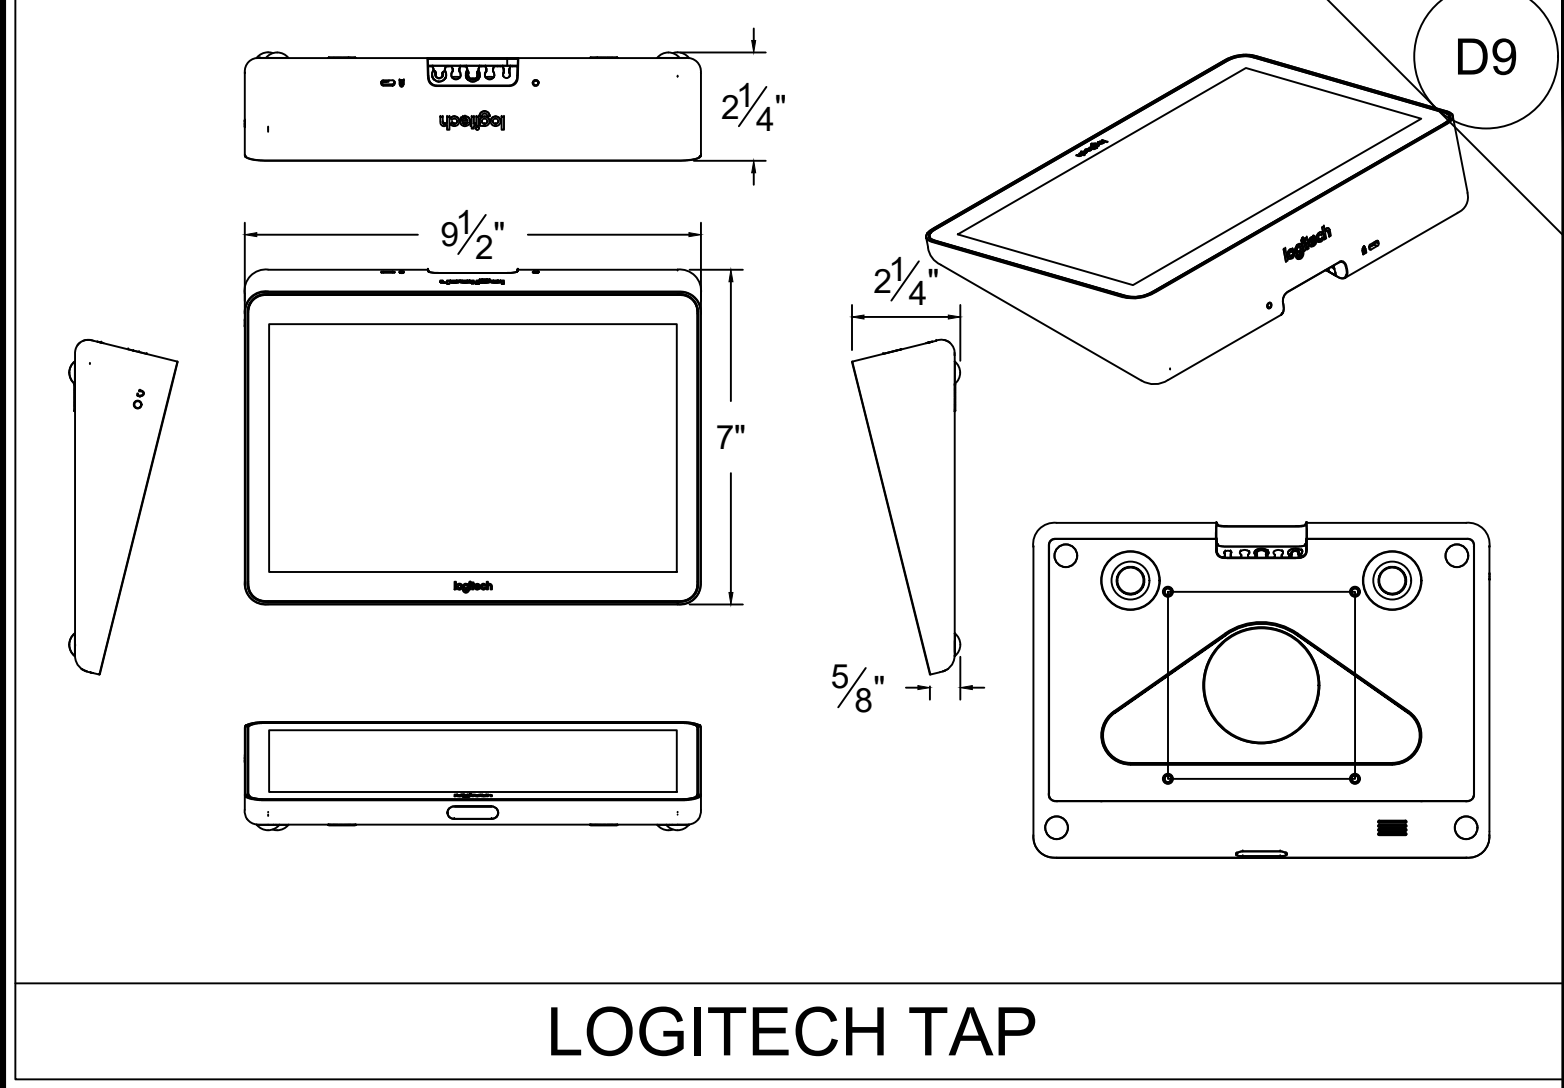

LOGITECH TAP

COMPANY

NEWTOWN
COMMUNITY CENTER

8 SIMPSON ST,
NEWTOWN, CT 06470

ARCHITECT

N/A

CONSULTANT

N/A

PREPARED & DESIGNED BY

VISIONPOINT

Bringing People Together to Work

152 Rockwell Rd. B6,
Newington, CT 06111
Phone: (860) 436-9673
Fax: (860) 436-9790

SEAL

NOT FOR
CONSTRUCTION

STATUS

☐ PROPOSAL

☐ SKETCH

☒ PRELIMINARY

☐ REFERENCE

☐ PROGRAMMING PHASE

☐ SCHEMATIC DESIGN PHASE

☐ DESIGN DEVELOPMENT PHASE

☐ CONSTRUCTION DOCUMENTS PHASE

☐ INTEGRATION

☐ AS BUILT

PROJECT INFORMATION

PROJECT NAME: NEWTOWN
COMMUNITY CENTER

PROJECT NUMBER: P1579

PROJECT START DATE: 08/05/2026

ENGINEERED BY: KR

DRAWN BY: AVDL

SALES: MO

PROJECT MANAGER: GA

CHECKED BY: DD & MG

SCALE: NONE

LEGAL NOTICE

COPYRIGHT 2026, VISIONPOINT LLC.
ALL DRAWINGS AND WRITTEN MATERIAL
HEREIN CONSTITUTE ORIGINAL AND
UNPUBLISHED WORK OF THE ENGINEER.
WRITTEN DIMENSIONS ON DRAWINGS
SHALL HAVE PRECEDENCE OVER SCALED
DIMENSIONS. CONTRACTORS SHALL
VERIFY AND BE RESPONSIBLE FOR
DIMENSIONS. VISIONPOINT LLC MUST BE
NOTIFIED OF ANY DEVIATIONS FROM
DIMENSIONS OR CONDITIONS OF SAID
DRAWINGS. SHOP DRAWINGS MUST BE
SUBMITTED FOR APPROVAL BEFORE
PROCEEDING.

STAMP

DATE:

BY:

This review is only for general conformance
with the design concept of the project and
general compliance with the information given
in the contract documents. Contractor is
responsible for dimension to be confirmed and
corrected of the project information that
pertains solely to the fabrication processes or
to the means, methods, techniques,
equipment, and procedures of construction;
coordination of fit of all trades, and for
performing all work in a safe and satisfactory
manner.

REVISION NUMBER

REVISION #1: XXXXXXXXXX

REVISION #2: XXXXXXXXXX

REVISION #3: XXXXXXXXXX

REVISION #4: XXXXXXXXXX

REVISION #5: XXXXXXXXXX

REVISION #6: XXXXXXXXXX

RELEASE DATE

08/05/2026

TITLE

AV DETAILS I

DRAWING

AV-D1.1